
A MOUNTAIN COURTYARD HOUSE

Weberman Residence: Spatial Study

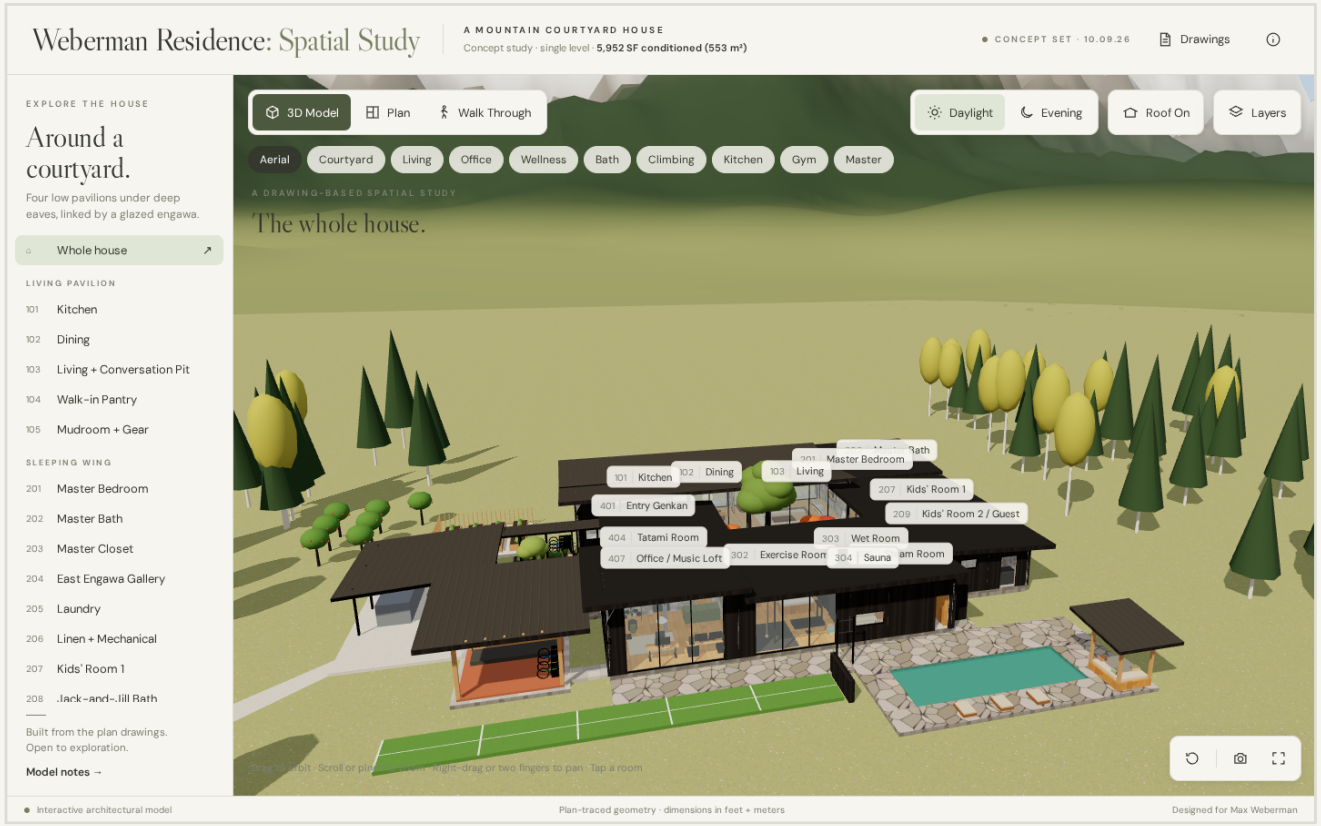

Aerial view from the live model, looking north toward the mountains.

Around a courtyard.

Four low pavilions under deep eaves, linked by a glazed engawa.

CONDITIONED AREA
5,952 SF · 553 m²

LEVELS
One (single-level courtyard plan)

FOOTPRINT
98' × 88' · 29.9 × 26.8 m

COURTYARD
44' × 33' · 13.4 × 10.1 m

BEDROOMS / BATHS
3 bedrooms · 3.5 baths

PREPARED
October 9, 2026 · for Max Weberman

INTERACTIVE 3D MODEL
https://webermanapps.github.io/weberman-residence/
https://github.com/WebermanApps/weberman-residence

Design Concept

One low house around one garden. Four single-storey pavilions wrap a 44 × 33 ft courtyard, the heart of the house. The **Living Pavilion** faces north to the mountains, the **Sleeping Wing** runs along the quiet east side, the **Wellness + Gym Wing** sits on the sunny south side next to the pool, and **Studio + Arrival** on the west holds the entry, tatami room and office / music loft. A glazed engawa ties them together, so every trip through the house runs along the garden.

Warm, low, open resort-modern. Deep 6 to 8 ft eaves, a butterfly roof over the living pavilion, and low standing-seam roofs elsewhere. Outside it is a black timber house: shou sugi ban cladding under standing-seam metal roofs, with a rammed-earth wall at the entry, flagstone terraces and a gravel drive. Inside: lime plaster, honey oak and oak herringbone, black stone, marble, green zellige, cedar and aspen. The room-by-room swipe decks removed white render, glass at the entry, timber decks, slat enclosures, flat roofs, wood-burning stoves, white hammams, glass shower enclosures, brass taps in the bath, bunk beds and wood headboards. No gables, logs, stone fireplaces, clay tile, freestanding tubs or koi ponds.

Fine, not showy. The craft is in the details: pocketing glass that disappears into the walls, slim black frames, a hinoki soaking tub under a skylight, cedar soffits, a 10-ft marble island against green zellige, and a sculpted wood ceiling over the music loft. There is one big mountain window rather than walls of glass everywhere.

Loved in the swipe test	Where it lives in the plan
Central courtyard as the heart	Shade tree with a curved teak bench, Japanese maples, raked gravel, a planted water court, stone lanterns and a basin
Engawa walkway	Glazed engawa on three sides; flagstone terrace under the eaves (no timber deck)
Deep eaves	6' to 8' overhangs, cedar soffits
Disappearing glass walls	Pocketing sliders from the living, dining and galleries to the courtyard
Big mountain-view window	28-ft fixed window in the living room; full-height glass in the master
Tatami room	8-mat room with a tokonoma, off the west engawa
Japanese soaking tub	Hinoki tub at the master bath corner window
Loft-like office	24' × 22' office / music loft with a 14' ceiling
Sauna + outdoor shower	Cedar sauna with backlit aspen benches and an electric heater, stone steam room, zellige plunge, pool and courtyard showers
Climbing wall	Kids' bouldering wall in an open-air Climbing Pavilion by the gym, sprint lane and bike rack
Liked: conversation pit, butterfly roof, pergola, fire pit, meadow	Sunken pit with a low modular sofa, butterfly roof, pergola dining, round stone fire pit, bale pavilion, meadow, vegetable garden and fruit trees

MATERIAL PALETTE



Floor Plan




Weberman Residence: Spatial Study

FLOOR PLAN · SINGLE LEVEL · SCALE AS NOTED

LIVING PAVILION		**1,728 SF**
101	Kitchen	384 SF / 35.7 m²
102	Dining	432 SF / 40.1 m²
103	Living + Conversation Pit	672 SF / 62.4 m²
104	Walk-in Pantry	120 SF / 11.1 m²
105	Mudroom + Gear	120 SF / 11.1 m²
SLEEPING WING		**1,824 SF**
201	Master Bedroom	336 SF / 31.2 m²
202	Master Bath	168 SF / 15.6 m²
203	Master Closet	120 SF / 11.1 m²
204	East Engawa Gallery	300 SF / 27.9 m²
205	Laundry	100 SF / 9.3 m²
206	Linen + Mechanical	100 SF / 9.3 m²
207	Kids' Room 1	220 SF / 20.4 m²
208	Jack-and-Jill Bath	160 SF / 14.9 m²
209	Kids' Room 2 / Guest	220 SF / 20.4 m²
210	Guest / Pool Bath	100 SF / 9.3 m²
211	Pool Equipment (uncond.)	100 SF / 9.3 m²
WELLNESS + GYM WING		**1,188 SF**
301	South Engawa Gallery	220 SF / 20.4 m²
302	Exercise Room	484 SF / 45.0 m²
303	Wet Room	208 SF / 19.3 m²
304	Sauna	72 SF / 6.7 m²
305	Steam Room	72 SF / 6.7 m²
306	Changing + Towels	132 SF / 12.3 m²
STUDIO + ARRIVAL		**1,212 SF**
401	Entry Genkan	144 SF / 13.4 m²
402	Coat + Shoe Closet	42 SF / 3.9 m²
403	Powder Room	42 SF / 3.9 m²
404	Tatami Room	156 SF / 14.5 m²
405	Instrument + AV Closet	72 SF / 6.7 m²
406	West Engawa Gallery	228 SF / 21.2 m²
407	Office / Music Loft	528 SF / 49.1 m²
COVERED OUTDOOR (NOT CONDITIONED)		**324 SF**
C1	Climbing Pavilion	324 SF / 30.1 m²
TOTAL CONDITIONED		**5,952 SF · 553 m²**

Areas measured to wall centerlines.
Footprint 98' × 88' (29.9 × 26.8 m) around a 44' × 33' courtyard.
Ceilings: living 12' butterfly with clerestory, office 14',
bedrooms 10-11', sauna/hammam 8'.
Glass shown in blue: pocketing sliders to the courtyard.
Not for construction. Concept study for discussion.

Site Plan

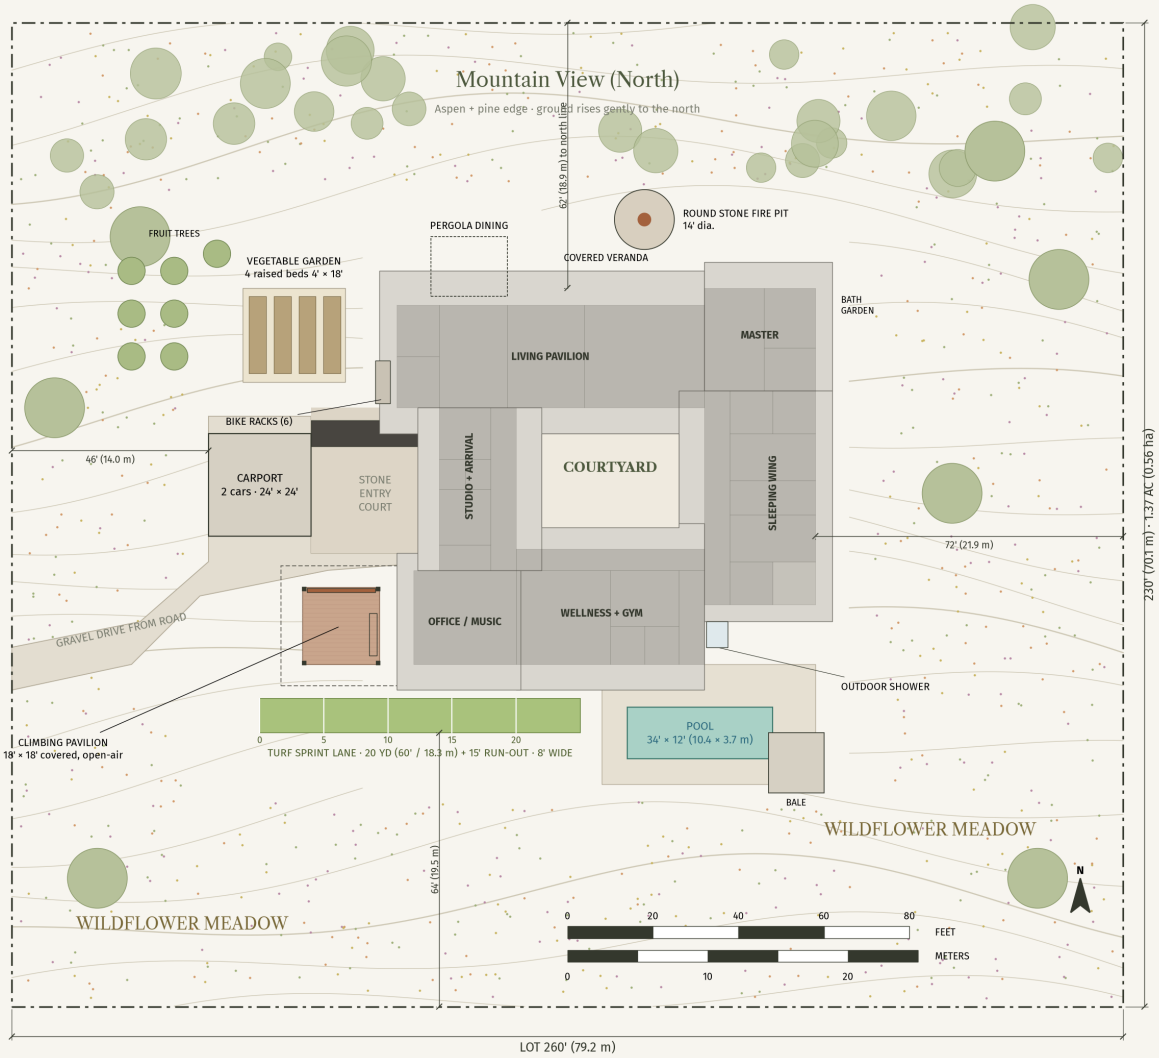

Weberman Residence: Spatial Study

SITE PLAN · MOUNTAIN PARCEL (ASSUMED)

LOT (ASSUMED)
260' × 230' · 1.37 ac · 0.56 ha

HOUSE FOOTPRINT
98' × 88' · 29.9 × 26.8 m

CONDITIONED AREA
5,952 SF · 553 m²

COURTYARD
44' × 33' · 13.4 × 10.1 m

POOL
34' × 12' · 10.4 × 3.7 m, 4'-5' deep

TURF SPRINT LANE
75' × 8' · 22.9 × 2.4 m (20 yd + run-out)

VEGETABLE GARDEN
24' × 22' · 4 raised beds

CARPORT
24' × 24' · modern black steel, covered walkway

FIRE PIT
Round stone, 14' dia., north terrace

PERGOLA DINING
18' × 14' off the kitchen

BIKE RACKS
6 at mudroom door + 4 at climbing pavilion

CLIMBING PAVILION
18' × 18' covered, open-air · soft-fall · not conditioned

OUTDOOR SHOWERS
By the pool + in the courtyard, charred-timber walls

POOL + BALE
Green stone tile, flagstone deck, bale pavilion

Orientation: the living pavilion and master suite face north to the mountains; the pool, gym and sprint lane get the sun on the south. The wildflower meadow wraps the house; aspen and pine screen the edges. Lot, grades and setbacks are assumed. Verify with a survey.

Room Program

Living Pavilion		Size	SF	m²
101	Kitchen	16' × 24'	384	35.7
102	Dining	18' × 24'	432	40.1
103	Living + Conversation Pit	28' × 24'	672	62.4
104	Walk-in Pantry	10' × 12'	120	11.1
105	Mudroom + Gear	10' × 12'	120	11.1
	Subtotal (conditioned)		**1,728**	**160.5**

Sleeping Wing		Size	SF	m²
201	Master Bedroom	14' × 24'	336	31.2
202	Master Bath	12' × 14'	168	15.6
203	Master Closet	12' × 10'	120	11.1
204	East Engawa Gallery	6' × 50'	300	27.9
205	Laundry	10' × 10'	100	9.3
206	Linen + Mechanical	10' × 10'	100	9.3
207	Kids' Room 1	20' × 11'	220	20.4
208	Jack-and-Jill Bath	20' × 8'	160	14.9
209	Kids' Room 2 / Guest	20' × 11'	220	20.4
210	Guest / Pool Bath	10' × 10'	100	9.3
211	Pool Equipment (uncond.)	10' × 10'	100	9.3
	Subtotal (conditioned)		**1,824**	**169.5**

Wellness + Gym Wing		Size	SF	m²
301	South Engawa Gallery	44' × 5'	220	20.4
302	Exercise Room	22' × 22'	484	45.0
303	Wet Room	16' × 13'	208	19.3
304	Sauna	8' × 9'	72	6.7
305	Steam Room	8' × 9'	72	6.7
306	Changing + Towels	6' × 22'	132	12.3
	Subtotal (conditioned)		**1,188**	**110.4**

Studio + Arrival		Size	SF	m²
401	Entry Genkan	12' × 12'	144	13.4
402	Coat + Shoe Closet	6' × 7'	42	3.9
403	Powder Room	6' × 7'	42	3.9
404	Tatami Room	12' × 13'	156	14.5
405	Instrument + AV Closet	12' × 6'	72	6.7
406	West Engawa Gallery	6' × 38'	228	21.2
407	Office / Music Loft	24' × 22'	528	49.1
	Subtotal (conditioned)		**1,212**	**112.6**

Covered Outdoor (Not Conditioned)		Size	SF	m²
C1	Climbing Pavilion	18' × 18'	324	30.1
	Subtotal (covered, open-air)		**324**	**30.1**


Total Conditioned **5,952 SF · 553 m²**

Excludes the Climbing Pavilion (covered outdoor), pool equipment room, carport, veranda, pergola and courtyar

Interactive Model Screenshots




Aerial: black timber pavilions under standing-seam roofs

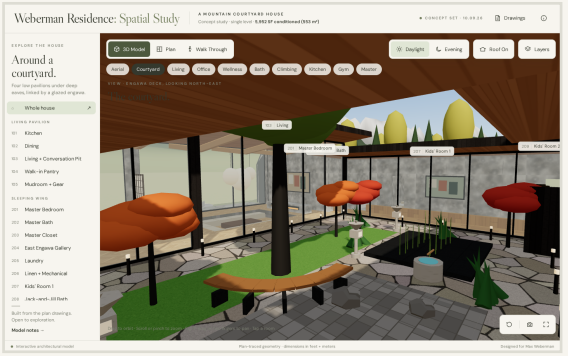

Courtyard: shade tree, teak bench, maples, lanterns, water court




Kitchen + living: marble island, zellige, herringbone, conversation pit

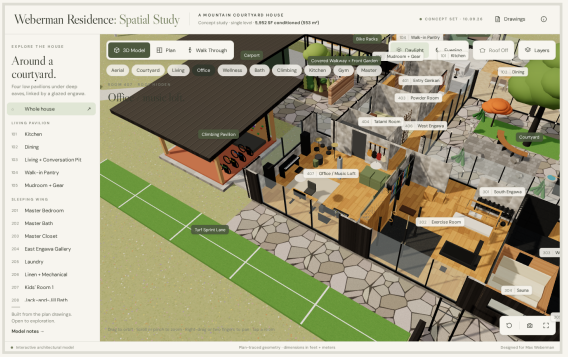

Office / music loft: sit-stand desk to the garden, studio desk, guitar wall




Gym: rig with rings and rope, Cadillac, reformer, rower, mirror wall

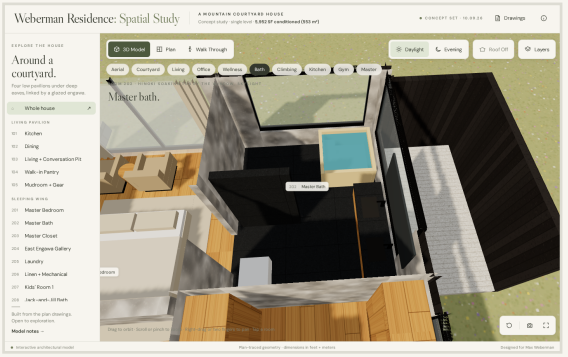

Master bath: hinoki tub by the window, black stone, skylight

Climbing Pavilion

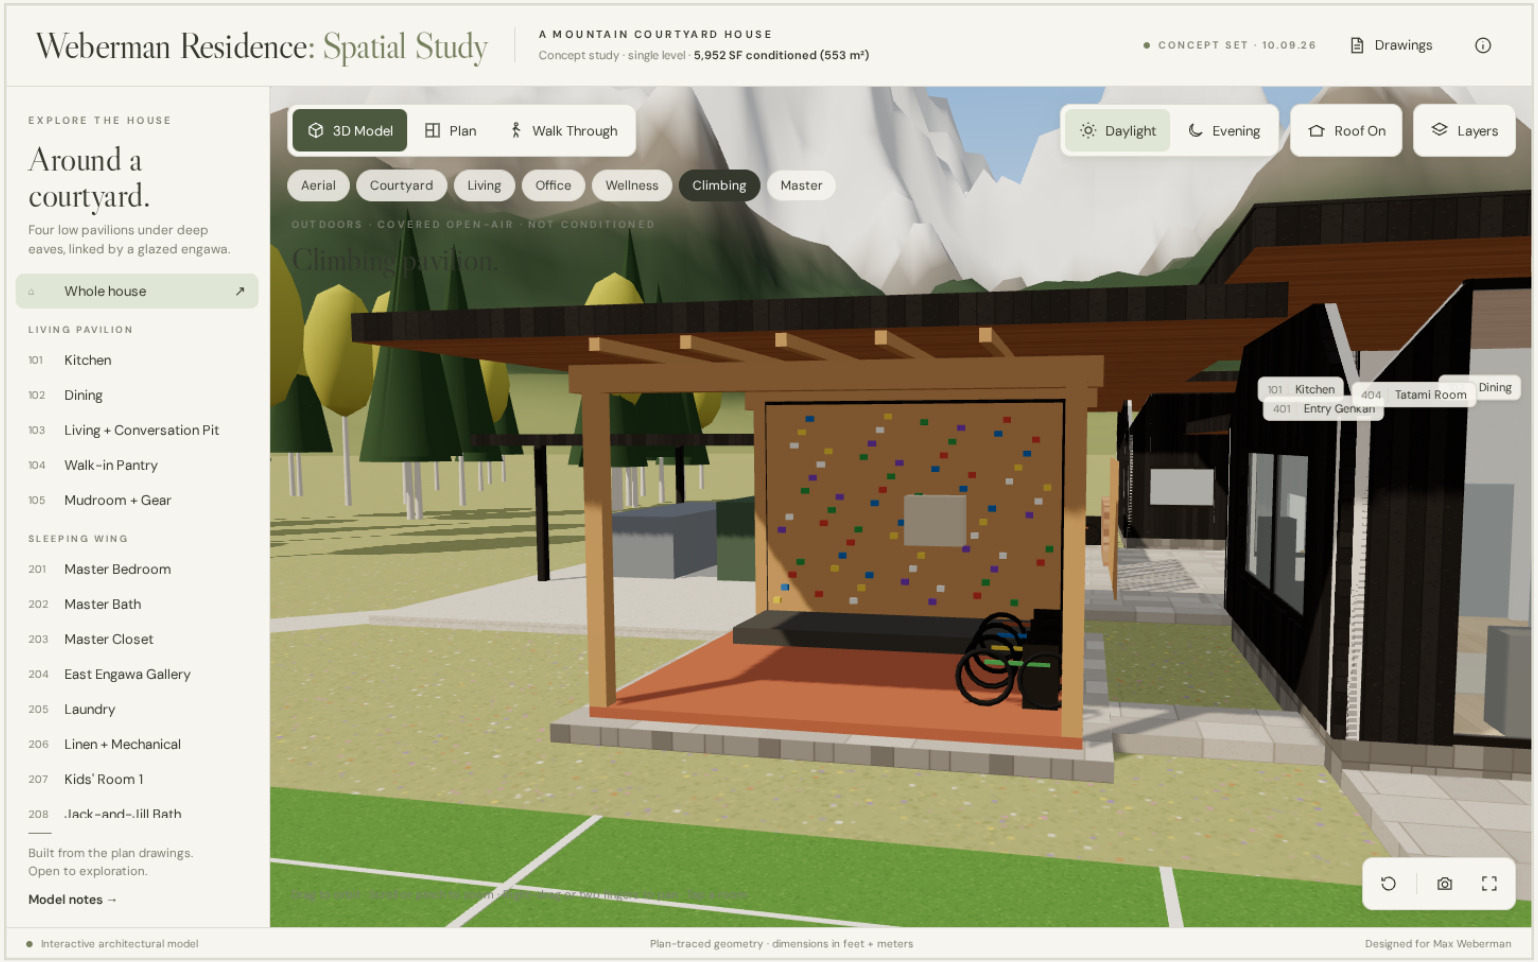

What changed. The kids' climbing wall left the exercise room and now has its own open-air pavilion, 18 × 18 ft (324 SF covered, not conditioned). It has a fir post-and-beam frame, a standing-seam roof with 5-ft eaves and a charred-timber fascia to match the house, and a poured-rubber soft-fall surface. A 16-ft-wide, 12-ft-high bouldering wall faces south onto the sprint lane, with a crash pad and a 4-bike rack. It sits just west of the office and exercise room, so the gym, lane, wall and bikes form one active zone. The gym's west wall is now a full-height storage wall with a wall-mounted rig and rings.

06 · LIVE MODEL ON A 390 × 844 PHONE VIEWPORT


Mobile Viewport



Aerial



Kitchen + living

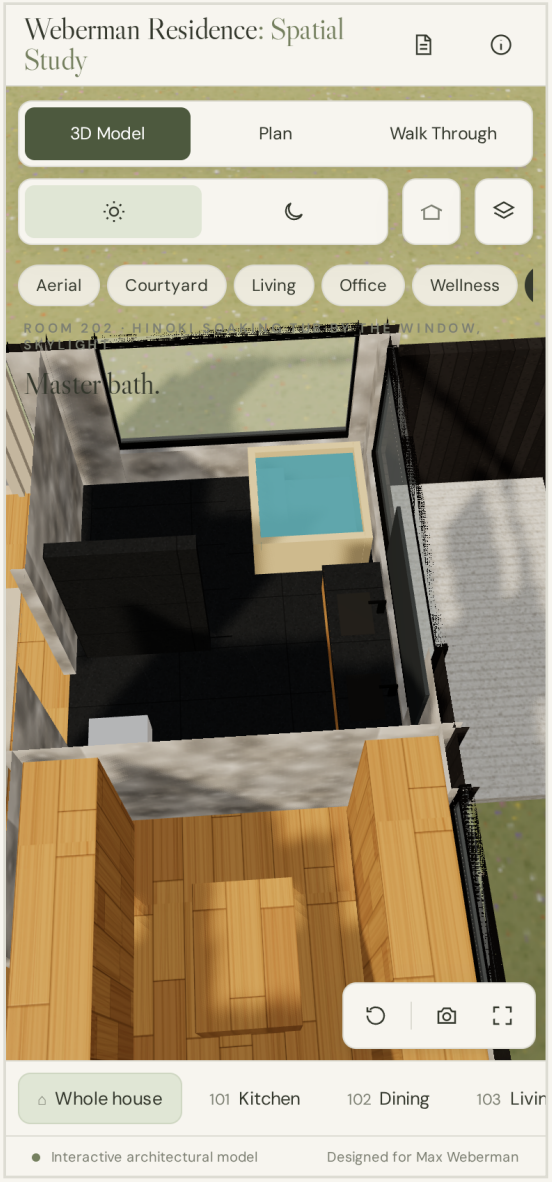

Master bath

Finish Schedule

Room	Floor	Finishes + key fixtures (from the room-by-room swipe decks)
101 Kitchen	Large-format limestone tiles	Large stone tiles; lime plaster; white handleless cabinets; black stone counters; green zellige backsplash; marble island; honey-oak open shelves; stainless range; glass chimney hood; white apron sink; brass faucet
102 Dining	Oak herringbone	Oak herringbone; lime plaster; exposed fir beams; cedar ceiling; honey-oak table; paper lantern
103 Living + Conversation Pit	Oak herringbone	Oak herringbone; lime plaster; exposed fir beams; cedar ceiling; linen pit upholstery; cognac leather; paper lanterns; shoji screens; art wall
104 Walk-in Pantry	Large-format limestone tiles	Large stone tiles; lime plaster; honey-oak open shelving
105 Mudroom + Gear	Large-format limestone tiles	Large stone tiles; lime plaster; honey-oak cubbies; stone dog wash
201 Master Bedroom	Wide-plank honey oak	Honey-oak floor; lime plaster; wood ceiling with cove lighting; sheer linen curtains; big ceiling fan; linen bed
202 Master Bath	Honed black stone	Black stone floor and shower wall; lime plaster; hinoki soaking tub; floating oak vanity, integrated basins; matte black taps; skylight
203 Master Closet	Wide-plank honey oak	Honey-oak floor and millwork; lime plaster
204 East Engawa Gallery	Wide-plank honey oak	Honey-oak floor; lime plaster; black steel sliding glass
205 Laundry	Honed limestone	Honed limestone; lime plaster; white cabinets
206 Linen + Mechanical	Sealed concrete	Sealed concrete; painted plaster
207 Kids' Room 1	Wide-plank honey oak	Honey-oak floor; calm white lime plaster; oak window seat with linen cushion; cube bins; bouldering panel
208 Jack-and-Jill Bath	Honed limestone	Honed limestone; white tile tub-shower; oak vanities
209 Kids' Room 2 / Guest	Wide-plank honey oak	Honey-oak floor; calm white lime plaster; oak window seat; cube bins; climbing panel
210 Guest / Pool Bath	Honed limestone	Honed limestone; tiled walk-in shower; oak vanity
211 Pool Equipment	Sealed concrete	Sealed concrete
301 South Engawa Gallery	Wide-plank honey oak	Honey-oak floor; lime plaster; black steel sliding glass
302 Exercise Room	Wide-plank honey oak	Honey-oak floor; rubber lifting tiles; lime plaster; high wood ceiling; mirror wall; black steel rig; wood rings
303 Wet Room	Honed black stone	Black stone floor and walls; green zellige plunge; teak bench
304 Sauna	Aspen duckboard	Cedar walls and ceiling; pale aspen tiered benches, backlit; aspen duckboard floor; electric rock heater
305 Steam Room	Honed black stone	Honed black stone floor, walls and heated bench
306 Changing + Towels	Honed limestone	Honed limestone; lime plaster; honey-oak lockers
401 Entry Genkan	Large-format limestone tiles	Large stone tiles; rammed-earth feature wall; lime plaster; charred-oak pivot door
402 Coat + Shoe Closet	Wide-plank honey oak	Honey-oak floor; oak millwork
403 Powder Room	Honed limestone	Honed limestone; lime plaster; integrated stone basin
404 Tatami Room	Tatami (8 mats)	Tatami; lime plaster; shoji; walnut tokonoma
405 Instrument + AV Closet	Wide-plank honey oak	Honey-oak floor; painted plaster
406 West Engawa Gallery	Wide-plank honey oak	Honey-oak floor; lime plaster; black steel sliding glass
407 Office / Music Loft	Wide-plank honey oak	Honey-oak floor; lime plaster; fabric acoustic panels; acoustic ceiling clouds; sculpted wood ceiling; skylight; layered pendants
Exterior	Flagstone terraces	Black charred-timber (shou sugi ban) cladding; standing-seam metal roofs, low mono-pitch and butterfly; rammed-earth entry wall; solid charred-oak pivot door
Courtyard	Flagstone, lawn, raked gravel	Big shade tree; Japanese maples; planted water court; stone lanterns; stone water basin; curved teak bench; lit path lights; courtyard shower

Finish Schedule (Continued)

Room	Floor	Finishes + key fixtures (from the room-by-room swipe decks)
Pool + bale	Flagstone deck	Green stone pool tile; teak and linen loungers; bale pavilion with honey-oak platform and standing-seam roof
Landscape	Meadow, gravel	Wildflower meadow; vegetable garden in cedar beds; fruit trees; round stone fire pit; front garden beds
Arrival	Gravel drive, flagstone	Modern black steel carport; covered walkway to the front door
Climbing Pavilion	Poured-rubber soft-fall	Fir frame; standing-seam roof; 16 x 12 ft bouldering wall
Active zone	Turf	Sprint lane; outdoor pull-up station in black steel

Open Design Questions for Max

Site and orientation. Is there a real parcel? The plan assumes the mountain view is to the north and a gentle slope. A view to the west or south would mean rotating the courtyard. A steeper lot could become the gentle split (living pavilion 2 to 3 steps down).

Size. At 5,952 SF this is generous. The three glazed engawa galleries add about 750 SF. Options: make the south engawa an open-air covered walkway (about -220 SF), trim the kids' rooms and office by 2 ft each, or drop the tatami room into the west engawa. Any of these gets toward 5,000 to 5,400 SF.

Garage. The plan shows an open two-car carport. Do you want an enclosed garage or a ski / bike workshop? It would sit beside the mudroom.

Guest strategy. Kids' Room 2 is the guest room and uses the Guest / Pool Bath across the engawa. Do you want a separate guest suite instead (for example, the tatami room with its own bath), or a casita by the pool?

Music room acoustics. How loud do you play, and do you record? Full isolation (room-in-room, floated floor, sound-lock vestibule) costs more than the double-stud walls assumed here.

Pool and pond. Keep a small chlorinated or salt pool, or switch to a natural swimming pond, which you liked in the swipe test? Cold plunge indoors only, or a second one outside?

Fire. The plan uses a slim linear gas fire in the living room (no stone fireplace) and a wood-burning sunken fire pit outside. Is that the right balance? Is a wood stove or sauna stove allowed in your wildfire zone?

Climate and snow. Deep, low eaves and a butterfly valley need snow-load engineering and heated valley gutters. Confirm the snow region, and whether you prefer a single low shed roof over the butterfly.

Climbing pavilion. The wall is now outdoors in its own covered pavilion (as drawn). What ages are the kids? That sets the wall height (12 ft drawn) and the fall zone. Should one side get roll-down screens or a heater for winter use?

Budget and level of finish. How far to push the details: hinoki, Calacatta, pocketing steel-framed glass, rammed earth? Each has a lower-cost stand-in.