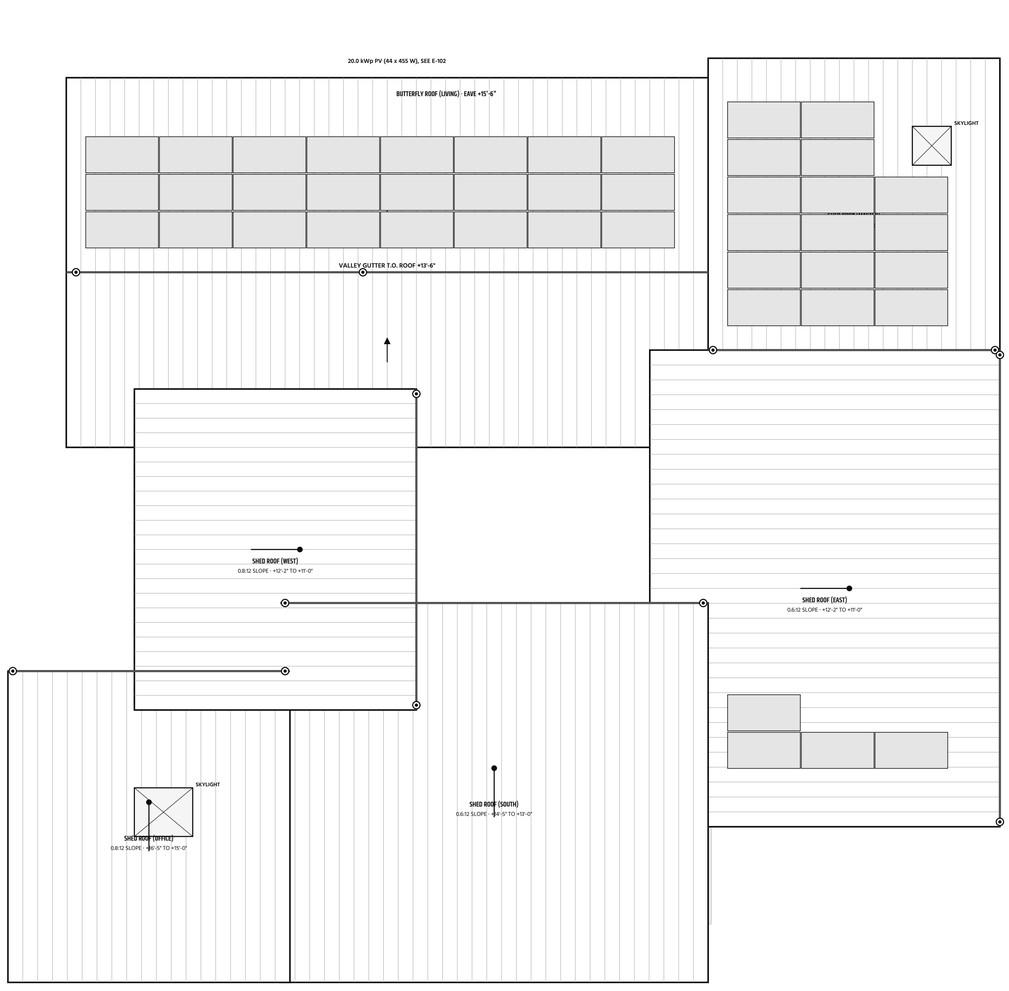

ROOF LEGEND

- Gutter, 150 x 125 mm AZ steel
- Downspout / rain chain to buried leader
- Valley gutter
- Standing seam at 450 mm
- Slope (dot = low side)

1 **ROOF PLAN**

SCALE: 1/8" = 1'-0"

WEBERMAN RESIDENCE

Mountain courtyard house, Thailand
Owner: Max Weberman

ISSUE

Design Development

NOT FOR CONSTRUCTION

DATE
11 Oct 2026

SCALE
1/8" = 1'-0"

MODEL
bim.json (from plan.json)

UNITS
Feet + inches (mm for members)

REVISION
DD-01

ROOF NOTES

Standing seam 0.5 mm AZ150, 75 mm PIR, vapor-open underlay on steel C-purlins (S-102).

Deep eaves 4-8 ft: cantilevered rafters; confirm for 0.6-1.0 kPa wind uplift (T15 / DPT 1.11).

All roofs drain to the rainwater ring (P-101) and two 19,000 L tanks.

SHEET TITLE

Roof Plan

SHEET

A-102