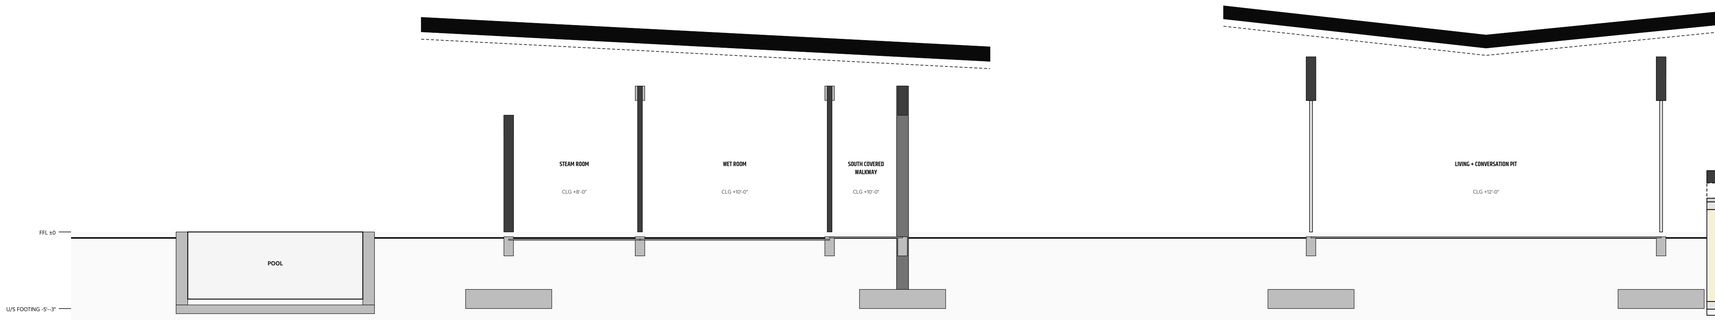

1 SECTION A-A (NORTH-SOUTH THROUGH LIVING, COURTYARD, WET ROOM, POOL)

SCALE: 3/16" = 1'-0"

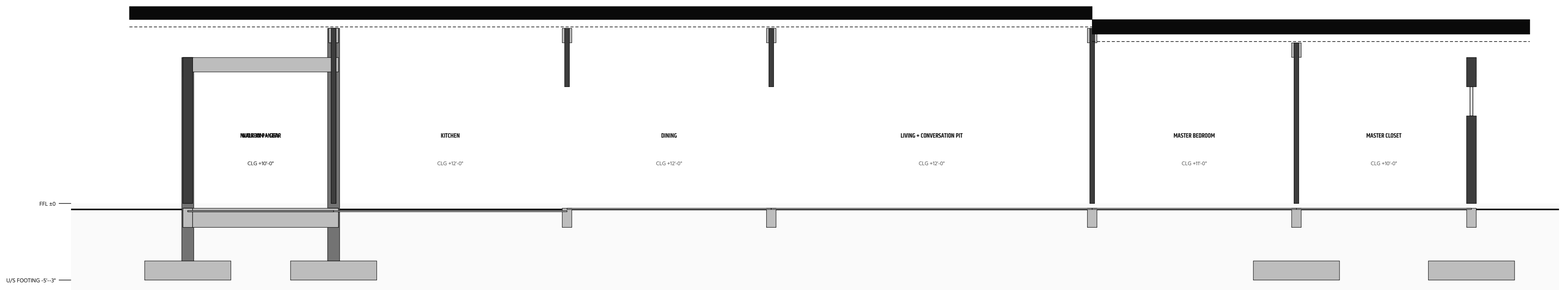

2 SECTION B-B (EAST-WEST THROUGH KITCHEN, DINING, LIVING, MASTER)

SCALE: 3/16" = 1'-0"

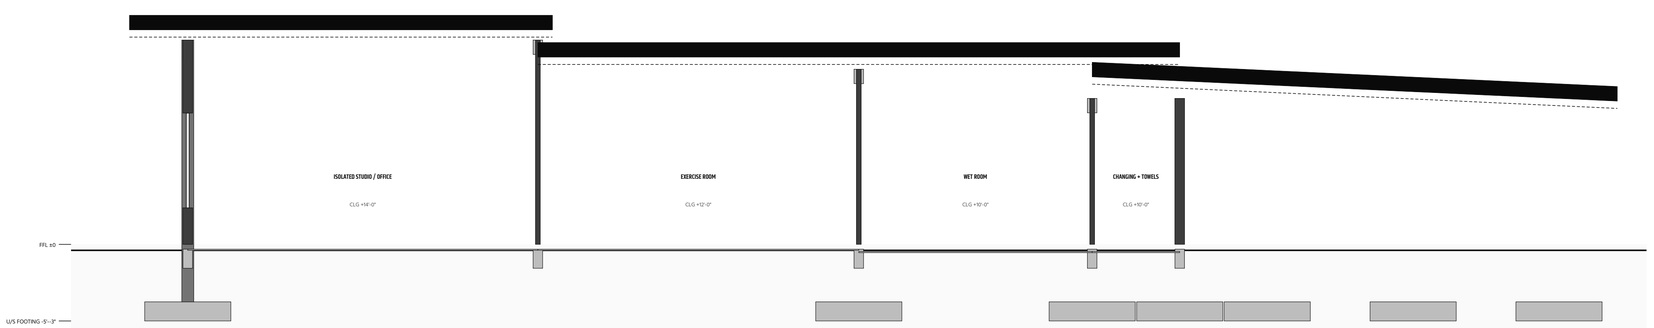

3 SECTION C-C (EAST-WEST THROUGH STUDIO, GYM, WET ROOM, CHANGING)

SCALE: 3/16" = 1'-0"

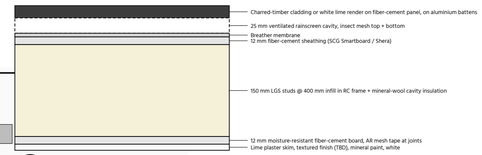

4 TYPICAL EXTERIOR WALL W1 (PLAN CUT, OUT TO IN)

SCALE: 1:10 (NTS)

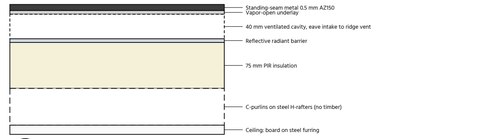

5 TYPICAL ROOF (TOP DOWN)

SCALE: 1:10 (NTS)

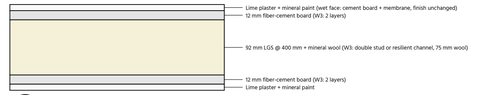

6 TYPICAL PARTITION W2 / W3

SCALE: 1:10 (NTS)

WEBERMAN RESIDENCE

Mountain courtyard house, Thailand
Owner: Max Weberman

ISSUE

Design Development

NOT FOR CONSTRUCTION

DATE
11 Oct 2026

SCALE
3/16" = 1'-0"

MODEL
bim.json (from plan.json)

UNITS
Feet + inches (mm for members)

REVISION
DD-01

SECTION NOTES

Section cuts at x = 60 ft (A), y = 67 ft (B) and y = 11 ft (C) in model coordinates; see key on S-101.

Footing depth 1.5–1.6 m assumed pending soil investigation.

Black = roof assembly; dashed = steel rafter zone; dark gray = walls cut; light gray = RC.

STANDARD

RC frame + LGS stud walls (fiber-cement, lime plaster) + steel roof.

Wet areas: membrane, flood test 24 h.

SHEET TITLE

Building Sections

SHEET

A-301