
A MOUNTAIN COURTYARD HOUSE

Weberman Residence: Spatial Study

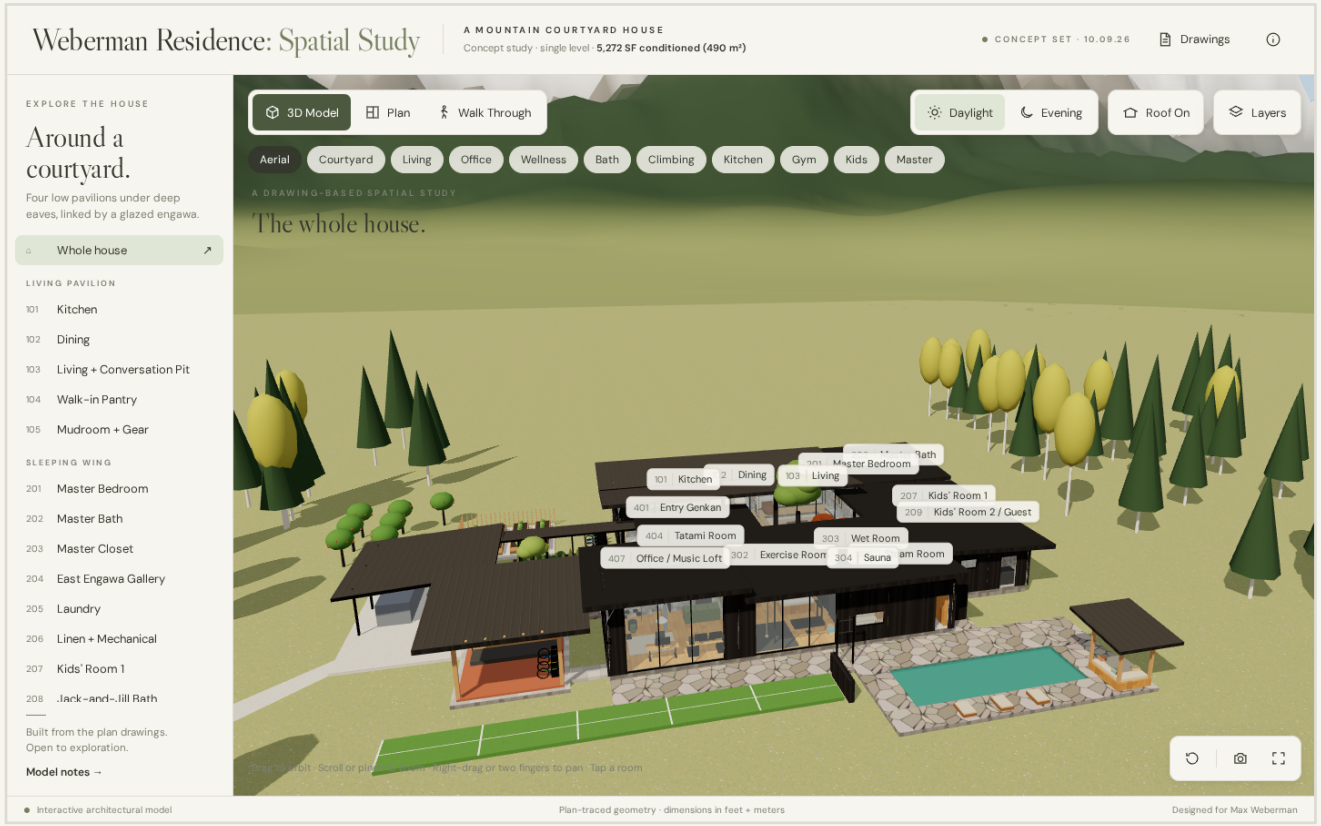

Aerial view from the live model, looking north toward the mountains.

CONDITIONED AREA
5,272 SF · 490 m²

LEVELS
One (single-level courtyard plan)

FOOTPRINT
94' × 83' · 28.7 × 25.3 m

COURTYARD
36' × 28' · 11.0 × 8.5 m

BEDROOMS / BATHS
3 bedrooms · 3.5 baths

PREPARED
October 9, 2026 · for Max Weberman

INTERACTIVE 3D MODEL
https://webermanapps.github.io/weberman-residence/
https://github.com/WebermanApps/weberman-residence

Design Concept

One low house around one garden. Four single-storey pavilions wrap a 36 × 28 ft courtyard, the heart of the house. The **Living Pavilion** faces north to the mountains, the **Sleeping Wing** runs along the quiet east side, the **Wellness + Gym Wing** sits on the sunny south side next to the pool, and **Studio + Arrival** on the west holds the entry, tatami room and office / music loft. A glazed engawa ties them together, so every trip through the house runs along the garden.

Warm, low, open resort-modern. Deep 6 to 8 ft eaves, a butterfly roof over the living pavilion, and low standing-seam roofs elsewhere. Outside it is a black timber house: shou sugi ban cladding under standing-seam metal roofs, with a rammed-earth wall at the entry, flagstone terraces and a gravel drive. Inside: lime plaster, honey oak and oak herringbone, black stone, marble, green zellige, cedar and aspen. The room-by-room swipe decks removed white render, glass at the entry, timber decks, slat enclosures, flat roofs, wood-burning stoves, white hammams, glass shower enclosures, brass taps in the bath, bunk beds and wood headboards. No gables, logs, stone fireplaces, clay tile, freestanding tubs or koi ponds.


Fine, not showy. The craft is in the details: pocketing glass that disappears into the walls, slim black frames, a hinoki soaking tub under a skylight, cedar soffits, a 10-ft marble island against green zellige, and a sculpted wood ceiling over the music loft. There is one big mountain window rather than walls of glass everywhere.

Loved in the swipe test	Where it lives in the plan
Central courtyard as the heart	Shade tree with a curved teak bench, Japanese maples, raked gravel, a planted water court, stone lanterns and a basin
Engawa walkway	Glazed engawa on the east and west, an open-air covered walkway on the south, and a flagstone terrace under the eaves
Deep eaves	6' to 8' overhangs, cedar soffits
Disappearing glass walls	Pocketing sliders from the living, dining and galleries to the courtyard
Big mountain-view window	20-ft fixed window in the living room; full-height glass in the master
Tatami room	8-mat room with a tokonoma, off the west engawa
Japanese soaking tub	Hinoki tub at the master bath corner window
Loft-like office	24' × 22' isolated studio / office (room-within-a-room, STC 60+) with a 14' ceiling
Sauna + outdoor shower	Cedar sauna with backlit aspen benches and an electric heater, stone steam room, zellige plunge, pool and courtyard showers
Climbing wall	Kids' bouldering wall in an open-air Climbing Pavilion by the gym, sprint lane and bike rack
Liked: conversation pit, butterfly roof, pergola, fire pit, meadow	Sunken pit with a low modular sofa, butterfly roof, pergola dining, round stone fire pit, bale pavilion, meadow, vegetable garden and fruit trees

MATERIAL PALETTE



Floor Plan

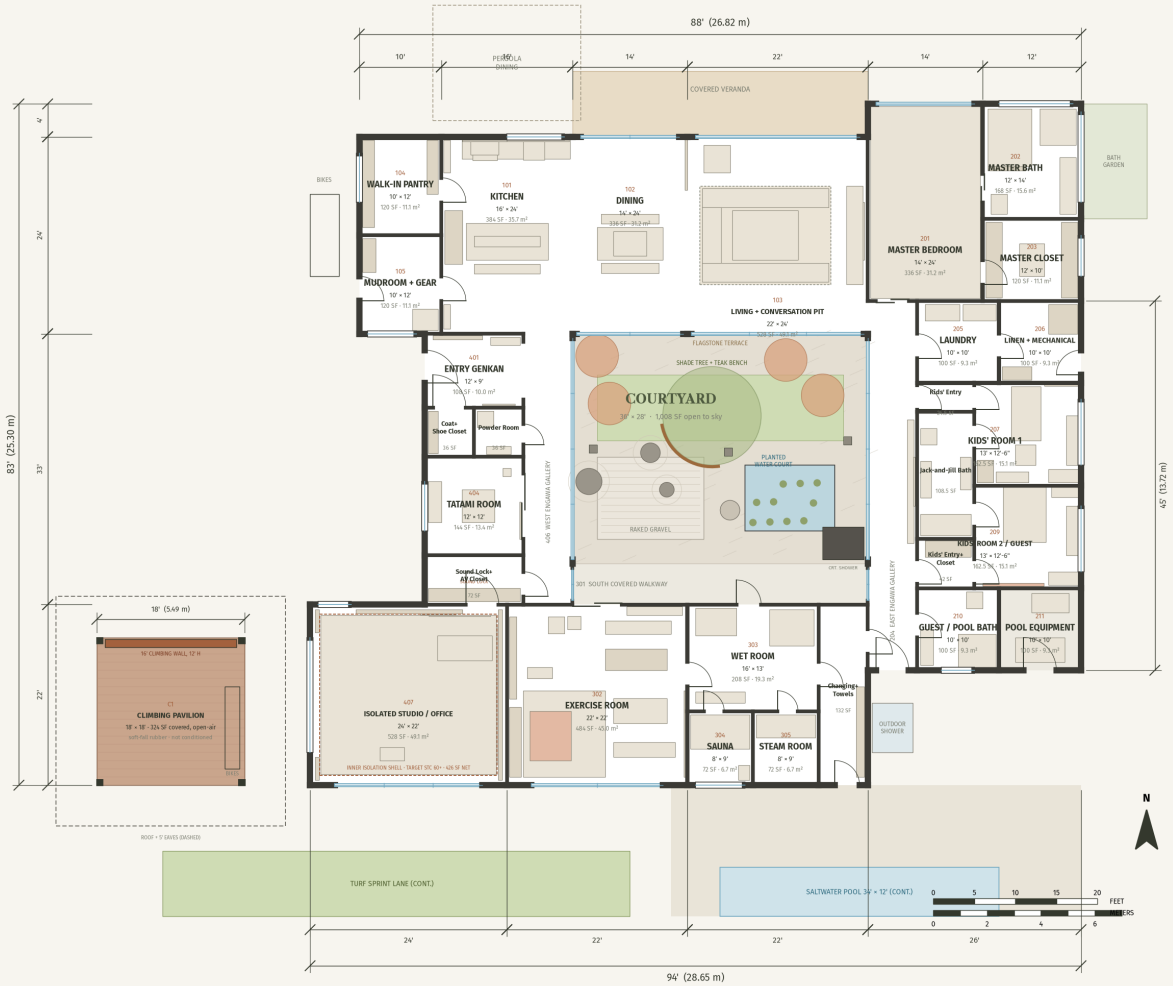


Weberman Residence: Spatial Study

FLOOR PLAN · SINGLE LEVEL · SCALE AS NOTED

LIVING PAVILION		**1,488 SF**
101	Kitchen	384 SF / 35.7 m²
102	Dining	336 SF / 31.2 m²
103	Living + Conversation Pit	528 SF / 49.1 m²
104	Walk-in Pantry	120 SF / 11.1 m²
105	Mudroom + Gear	120 SF / 11.1 m²
SLEEPING WING		**1,694 SF**
201	Master Bedroom	336 SF / 31.2 m²
202	Master Bath	168 SF / 15.6 m²
203	Master Closet	120 SF / 11.1 m²
204	East Engawa Gallery	270 SF / 25.1 m²
205	Laundry	100 SF / 9.3 m²
206	Linen + Mechanical	100 SF / 9.3 m²
207	Kids' Room 1	162.5 SF / 15.1 m²
208	Jack-and-Jill Bath	108.5 SF / 10.1 m²
209	Kids' Room 2 / Guest	162.5 SF / 15.1 m²
210	Guest / Pool Bath	100 SF / 9.3 m²
211	Pool Equipment (uncond.)	100 SF / 9.3 m²
212	Kids' Entry + Closet	42 SF / 3.9 m²
213	Kids' Entry	24.5 SF / 2.3 m²
WELLNESS + GYM WING		**968 SF**
301	South Covered Walkway (uncond.)	180 SF / 16.7 m²
302	Exercise Room	484 SF / 45.0 m²
303	Wet Room	208 SF / 19.3 m²
304	Sauna	72 SF / 6.7 m²
305	Steam Room	72 SF / 6.7 m²
306	Changing + Towels	132 SF / 12.3 m²
STUDIO + ARRIVAL		**1,122 SF**
401	Entry Genkan	108 SF / 10.0 m²
402	Coat + Shoe Closet	36 SF / 3.3 m²
403	Powder Room	36 SF / 3.3 m²
404	Tatami Room	144 SF / 13.4 m²
405	Sound Lock + AV Closet	72 SF / 6.7 m²
406	West Engawa Gallery	198 SF / 18.4 m²
407	Isolated Studio / Office	528 SF / 49.1 m²
COVERED OUTDOOR (NOT CONDITIONED)		**324 SF**
C1	Climbing Pavilion	324 SF / 30.1 m²
TOTAL CONDITIONED		**5,272 SF · 490 m²**

Areas measured to wall centerlines.
Footprint 94' × 83' (28.7 × 25.3 m) around a 36' × 28' courtyard.
Ceilings: living 12' butterfly with clerestory, office 14', bedrooms 10-11', sauna/steam 8'.
Glass shown in blue: pocketing sliders to the courtyard.
Not for construction. Concept study for discussion.

Site Plan

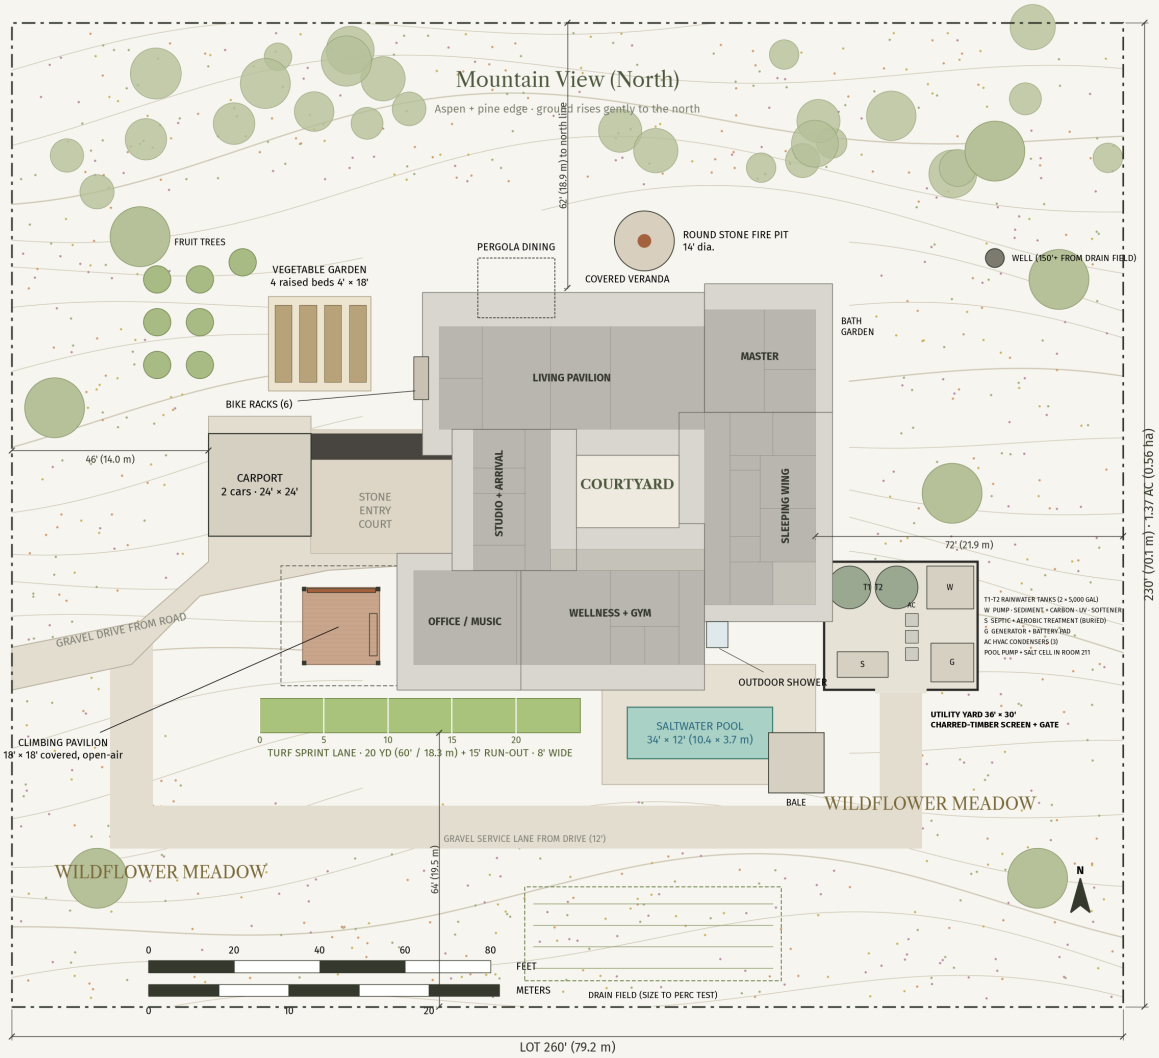

Weberman Residence: Spatial Study

SITE PLAN · MOUNTAIN PARCEL (ASSUMED)

LOT (ASSUMED)
260' × 230' · 1.37 ac · 0.56 ha

HOUSE FOOTPRINT
94' × 83' · 28.7 × 25.3 m

CONDITIONED AREA
5,272 SF · 490 m²

COURTYARD
36' × 28' · 11.0 × 8.5 m

POOL
34' × 12' · 10.4 × 3.7 m, 4'-5' deep

TURF SPRINT LANE
75' × 8' · 22.9 × 2.4 m (20 yd + run-out)

VEGETABLE GARDEN
24' × 22' · 4 raised beds

CARPORT
24' × 24' open · decided, no change

FIRE PIT
Round stone, 14' dia., north terrace

PERGOLA DINING
18' × 14' off the kitchen

BIKE RACKS
6 at mudroom door + 4 at climbing pavilion

CLIMBING PAVILION
18' × 18' · 12' wall · 17' roof · soft-fall · not conditioned

OUTDOOR SHOWERS
By the pool + in the courtyard, charred-timber walls

SALTWATER POOL + BALE
Salt cell (3-5 yr), sealed flagstone, 316 fittings

UTILITY YARD
36' × 30' screened · tanks, treatment, ATU, power, AC

WASTEWATER
Drain field S meadow · well up-slope NE

Orientation: the living pavilion and master suite face north to the mountains; the pool, gym and sprint lane get the sun on the south. The wildflower meadow wraps the house; aspen and pine screen the edges. Lot, grades and setbacks are assumed. Verify with a survey.

Room Program

Living Pavilion		Size	SF	m²
101	Kitchen	16' × 24'	384	35.7
102	Dining	14' × 24'	336	31.2
103	Living + Conversation Pit	22' × 24'	528	49.1
104	Walk-in Pantry	10' × 12'	120	11.1
105	Mudroom + Gear	10' × 12'	120	11.1
	Subtotal (conditioned)		**1,488**	**138.2**

Sleeping Wing		Size	SF	m²
201	Master Bedroom	14' × 24'	336	31.2
202	Master Bath	12' × 14'	168	15.6
203	Master Closet	12' × 10'	120	11.1
204	East Engawa Gallery	6' × 45'	270	25.1
205	Laundry	10' × 10'	100	9.3
206	Linen + Mechanical	10' × 10'	100	9.3
207	Kids' Room 1	13' × 12.5'	162.5	15.1
208	Jack-and-Jill Bath	7' × 15.5'	108.5	10.1
209	Kids' Room 2 / Guest	13' × 12.5'	162.5	15.1
210	Guest / Pool Bath	10' × 10'	100	9.3
211	Pool Equipment (uncond.)	10' × 10'	100	9.3
212	Kids' Entry + Closet	7' × 6'	42	3.9
213	Kids' Entry	7' × 3.5'	24.5	2.3
	Subtotal (conditioned)		**1,694**	**157.4**

Wellness + Gym Wing		Size	SF	m²
301	South Covered Walkway (uncond.)	36' × 5'	180	16.7
302	Exercise Room	22' × 22'	484	45.0
303	Wet Room	16' × 13'	208	19.3
304	Sauna	8' × 9'	72	6.7
305	Steam Room	8' × 9'	72	6.7
306	Changing + Towels	6' × 22'	132	12.3
	Subtotal (conditioned)		**968**	**89.9**

Studio + Arrival		Size	SF	m²
401	Entry Genkan	12' × 9'	108	10.0
402	Coat + Shoe Closet	6' × 6'	36	3.3
403	Powder Room	6' × 6'	36	3.3
404	Tatami Room	12' × 12'	144	13.4
405	Sound Lock + AV Closet	12' × 6'	72	6.7
406	West Engawa Gallery	6' × 33'	198	18.4
407	Isolated Studio / Office	24' × 22'	528	49.1
	Subtotal (conditioned)		**1,122**	**104.2**

Covered Outdoor (Not Conditioned)		Size	SF	m²
C1	Climbing Pavilion	18' × 18'	324	30.1
	Subtotal (covered, open-air)		**324**	**30.1**

Total Conditioned **5,272 SF · 490 m²**

Excludes the Climbing Pavilion and South Covered Walkway (covered outdoor), pool equipment room, carport, v

Interactive Model Screenshots



Aerial: black timber pavilions under standing-seam roofs



Courtyard: shade tree, teak bench, maples, lanterns, water court




Kitchen + living: marble island, zellige, herringbone, conversation pit



Office / music loft: sit-stand desk to the garden, studio desk, guitar wall



Gym: rig with rings and rope, Cadillac, reformer, rower, mirror wall

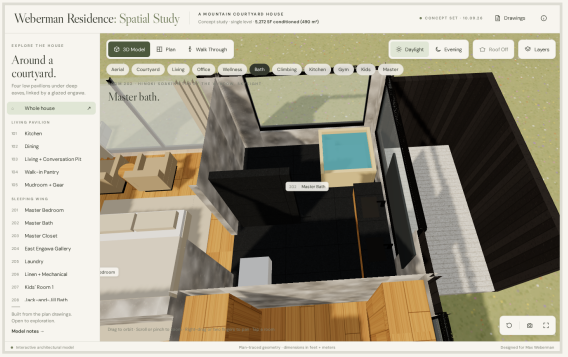


Master bath: hinoki tub by the window, black stone, skylight

Size Reduction

Room	Before	SF	After	SF	Change
102 Dining	18' × 24'	432	14' × 24'	336	-96
103 Living + Conversation Pit	28' × 24'	672	22' × 24'	528	-144
207 Kids' Room 1	20' × 11'	220	13' × 12.5'	162.5	-57.5
208 Jack-and-Jill Bath	20' × 8'	160	7' × 15.5'	108.5	-51.5
209 Kids' Room 2 / Guest	20' × 11'	220	13' × 12.5'	162.5	-57.5
204 East Engawa Gallery	6' × 50'	300	6' × 45'	270	-30
406 West Engawa Gallery	6' × 38'	228	6' × 33'	198	-30
301 South Covered Walkway (now open-air)	44' × 5'	220	36' × 5'	0	-220
401 Entry Genkan	12' × 12'	144	12' × 9'	108	-36
402 Coat + Shoe Closet	6' × 7'	42	6' × 6'	36	-6
403 Powder Room	6' × 7'	42	6' × 6'	36	-6
404 Tatami Room	12' × 13'	156	12' × 12'	144	-12
212 Kids' Entry + Closet	-	0	7' × 6'	42	+42
213 Kids' Entry	-	0	7' × 3.5'	24.5	+24.5
Courtyard (open to sky)	44' × 33'	1,452	36' × 28'	1,008	-444
Total conditioned		5,952		5,272	-680

What stayed the same. The master suite, office / studio, exercise room and wellness wing (wet room, sauna, steam room, changing) keep their sizes. The master suite moved 5 ft south with the living pavilion, and the west wing moved 8 ft east to close up the courtyard. Kitchen (16 × 24) and the 16 × 12 conversation pit are unchanged. The galleries shortened with the courtyard; the west wing rooms lost 5 ft of length to match (tatami is now a true 12 × 12 eight-mat room). The south gallery became an open-air covered walkway under the wellness-wing eave.


Climbing Pavilion

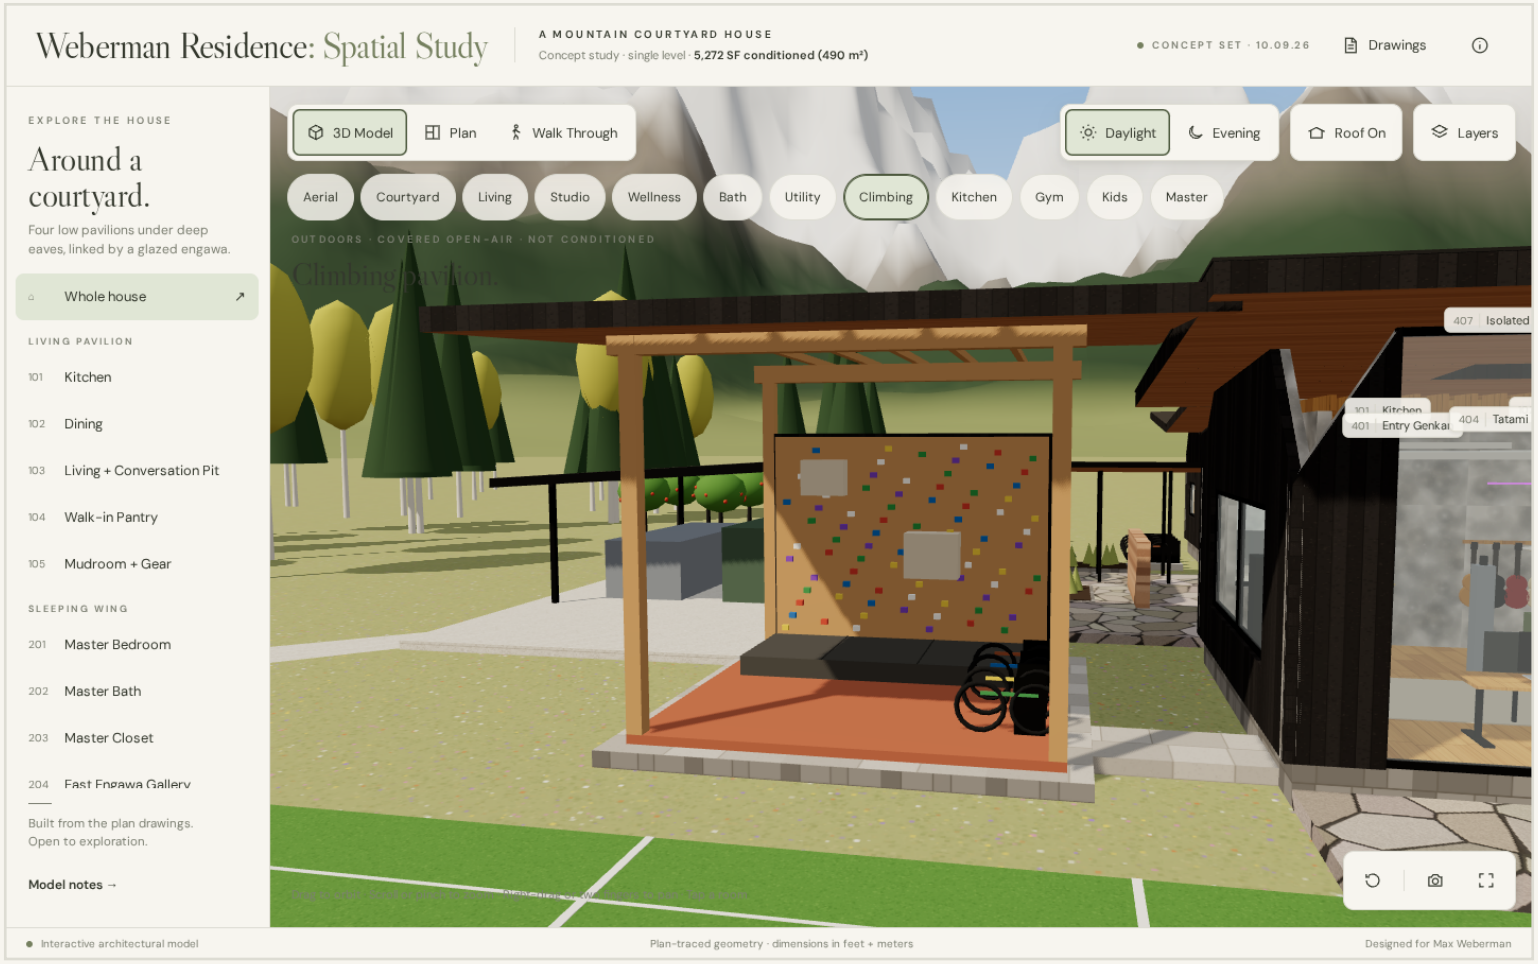

What changed. The kids' climbing wall left the exercise room and now has its own open-air pavilion, 18 × 18 ft (324 SF covered, not conditioned). It has a fir post-and-beam frame, a standing-seam roof with 5-ft eaves and a charred-timber fascia to match the house, and a poured-rubber soft-fall surface. Decided 10.10.26: a full 16-ft-wide, 12-ft-high climbing wall from day one faces south onto the sprint lane, over soft-fall and thick crash pads, with a 4-bike rack. The roof was raised to 17 ft, so the beams clear the top of the wall by about 3 ft and the roof by about 4 ft. It sits just west of the office and exercise room, so the gym, lane, wall and bikes form one active zone. The gym's west wall is now a full-height storage wall with a wall-mounted rig and rings.

06 · LIVE MODEL ON A 390 × 844 PHONE VIEWPORT


Mobile Viewport

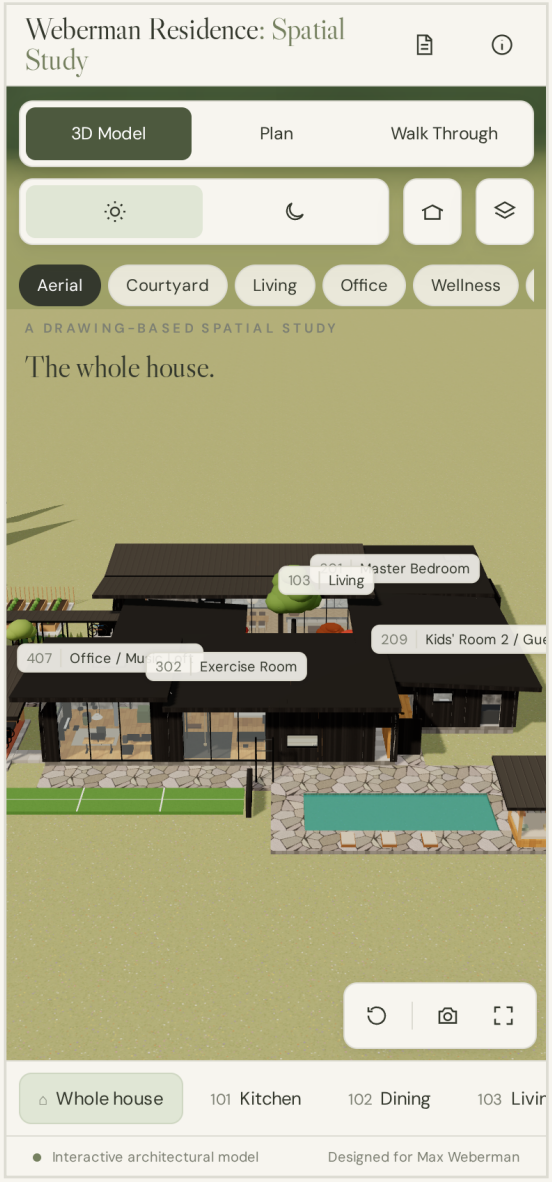

Aerial



Kitchen + living

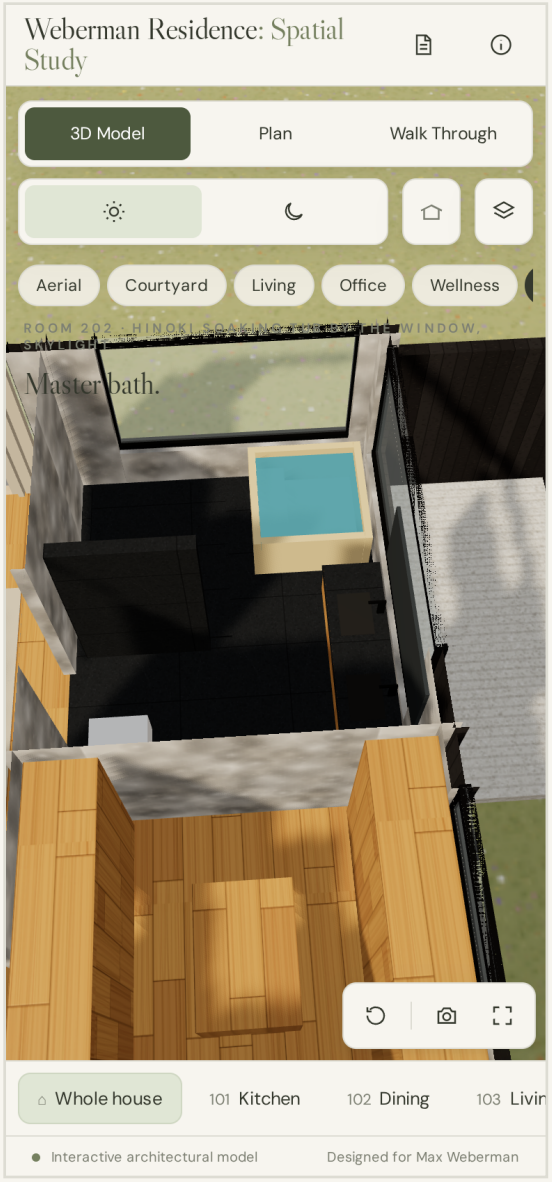

Master bath

Finish Schedule

Room	Floor	Finishes + key fixtures (from the room-by-room swipe decks)
101 Kitchen	Large-format limestone tiles	Large stone tiles; lime plaster; white handleless cabinets; black stone counters; green zellige backsplash; marble island; honey-oak open shelves; stainless range; glass chimney hood; white apron sink; brass faucet
102 Dining	Oak herringbone	Oak herringbone; lime plaster; exposed fir beams; cedar ceiling; honey-oak table for eight; paper lantern
103 Living + Conversation Pit	Oak herringbone	Oak herringbone; lime plaster; exposed fir beams; cedar ceiling; linen pit upholstery; cognac leather; paper lanterns; shoji screens; art wall
104 Walk-in Pantry	Large-format limestone tiles	Large stone tiles; lime plaster; honey-oak open shelving
105 Mudroom + Gear	Large-format limestone tiles	Large stone tiles; lime plaster; honey-oak cubbies; stone dog wash
201 Master Bedroom	Wide-plank honey oak	Honey-oak floor; lime plaster; wood ceiling with cove lighting; sheer linen curtains; big ceiling fan; linen bed
202 Master Bath	Honed black stone	Black stone floor and shower wall; lime plaster; hinoki soaking tub; floating oak vanity, integrated basins; matte black taps; skylight
203 Master Closet	Wide-plank honey oak	Honey-oak floor and millwork; lime plaster
204 East Engawa Gallery	Wide-plank honey oak	Honey-oak floor; lime plaster; black steel sliding glass
205 Laundry	Honed limestone	Honed limestone; lime plaster; white cabinets
206 Linen + Mechanical	Sealed concrete	Sealed concrete; painted plaster
207 Kids' Room 1	Wide-plank honey oak	Honey-oak floor; calm white lime plaster; oak window seat with linen cushion; oak wardrobe; cube bins; bouldering panel
208 Jack-and-Jill Bath	Honed limestone	Honed limestone; white tile tub-shower; oak vanities
209 Kids' Room 2 / Guest	Wide-plank honey oak	Honey-oak floor; calm white lime plaster; oak window seat; cube bins; climbing panel
210 Guest / Pool Bath	Honed limestone	Honed limestone; tiled walk-in shower; oak vanity
211 Pool Equipment	Sealed concrete	Sealed concrete
212 Kids' Entry + Closet	Wide-plank honey oak	Honey-oak floor; lime plaster; oak wardrobe
213 Kids' Entry	Wide-plank honey oak	Honey-oak floor; lime plaster
301 South Covered Walkway	Flagstone (open-air)	Flagstone floor; open-air, covered by the wellness-wing roof; cedar soffit
302 Exercise Room	Wide-plank honey oak	Honey-oak floor; rubber lifting tiles; lime plaster; high wood ceiling; mirror wall; black steel rig; wood rings
303 Wet Room	Honed black stone	Black stone floor and walls; green zellige plunge; teak bench
304 Sauna	Aspen duckboard	Cedar walls and ceiling; pale aspen tiered benches, backlit; aspen duckboard floor; electric rock heater
305 Steam Room	Honed black stone	Honed black stone floor, walls and heated bench
306 Changing + Towels	Honed limestone	Honed limestone; lime plaster; honey-oak lockers
401 Entry Genkan	Large-format limestone tiles	Large stone tiles; rammed-earth feature wall; lime plaster; charred-oak pivot door
402 Coat + Shoe Closet	Wide-plank honey oak	Honey-oak floor; oak millwork
403 Powder Room	Honed limestone	Honed limestone; lime plaster; integrated stone basin
404 Tatami Room	Tatami (8 mats)	Tatami; lime plaster; shoji; walnut tokonoma
405 Sound Lock + AV Closet	Wide-plank honey oak	Honey-oak floor; painted plaster; two solid-core doors with perimeter + drop seals
406 West Engawa Gallery	Wide-plank honey oak	Honey-oak floor; lime plaster; black steel sliding glass
407 Isolated Studio / Office	Wide-plank honey oak	Floated honey-oak floor on isolation pads; decoupled inner walls on resilient mounts; isolated ceiling; laminated double glazing; solid-core doors with seals; lined ducts; lime plaster; fabric acoustic panels; acoustic ceiling clouds; sculpted wood ceiling; skylight; layered pendants

Finish Schedule (Continued)

Room	Floor	Finishes + key fixtures (from the room-by-room swipe decks)
Exterior	Flagstone terraces	Black charred-timber (shou sugi ban) cladding; standing-seam metal roofs, low mono-pitch and butterfly; rammed-earth entry wall; solid charred-oak pivot door
Courtyard	Flagstone, lawn, raked gravel	Big shade tree; Japanese maples; planted water court; stone lanterns; stone water basin; curved teak bench; lit path lights; courtyard shower
Saltwater pool + bale	Sealed flagstone deck (salt-resistant penetrating sealer)	Saltwater pool with salt chlorine generator (cell replaced about every 3-5 years); marine-grade 316 stainless fittings, ladders and drains; green stone pool tile; teak and linen loungers; bale pavilion with honey-oak platform and standing-seam roof
Landscape	Meadow, gravel	Wildflower meadow; vegetable garden in cedar beds; fruit trees; round stone fire pit; front garden beds
Arrival	Gravel drive, flagstone	Modern black steel carport; covered walkway to the front door
Climbing Pavilion	Poured-rubber soft-fall + crash pads	Fir frame; standing-seam roof raised to 17 ft (about 4 ft clear over the wall); full 16 ft wide x 12 ft high climbing wall
Utility Yard	Compacted gravel + concrete equipment pads	7 ft charred-timber screen with service gate; 2 rainwater tanks; water treatment lean-to; septic/ATU lids; generator + battery pad; HVAC condensers
Active zone	Turf	Sprint lane; outdoor pull-up station in black steel

Decisions Log

#	Question	Decision	What changed in the design
1	Garage vs. carport	Keep the open carport	No change. Modern black steel two-car carport with a standing-seam roof and covered walkway to the front door.
2	Music room acoustics	Fully isolated studio	Office / music loft (407) becomes a room-within-a-room: decoupled inner stud walls on resilient isolation mounts, a floated floor on isolation pads, an isolated ceiling on spring hangers, laminated double glazing with an air gap, and quiet decoupled HVAC with lined ducts and silencers, plus acoustic panels and ceiling clouds inside. Target STC 60+ (about 60-65 dB isolation), NC-20 inside. Room 405 becomes a sound lock with two solid-core sealed doors; the studio's outside door was removed. About 14 in of build-up per side: 528 SF gross, about 426 SF net (21 ft 8 in x 19 ft 8 in). Gross conditioned area is unchanged. Furniture moved in off the inner walls, so it still works as an office: sit-stand desk facing the garden, studio desk, piano, drums, guitar wall and sofa.
3	Pool type	Small saltwater pool	Same 34 x 12 ft pool. A salt chlorine generator in the Pool Equipment room (211); replace the cell about every 3-5 years. Sealed flagstone deck (salt-resistant penetrating sealer, resealed every 2-3 years) and marine-grade 316 stainless fittings, ladders and drains.
4	Climbing wall height	Full 12 ft wall from day one	The full 16 ft wide x 12 ft high wall is built from the start (no low wall, no future extension). Poured-rubber soft-fall plus thick crash pads, a second upper volume, and more holds. The pavilion roof went up from 13 ft to 17 ft so the beams clear the top of the wall by about 3 ft and the roof by about 4 ft.
5	Utilities	New screened utility yard	36 x 30 ft yard beside the Pool Equipment room and wellness wing, behind a 7 ft charred-timber screen with a 12 ft service gate on a new gravel service lane from the drive. Inside: two rainwater tanks (about 5,000 gal each, fed from the roofs, with well or municipal backup), a water treatment lean-to (pressure pump, sediment + carbon filters, UV, softener), a buried septic tank + aerobic treatment unit, a generator + battery pad, and three HVAC condensers. Pool pump, filter and salt cell stay in room 211 next door. Drain field in the south meadow, more than 100 ft from the vegetable garden and the well; well up-slope to the north-east.

Open Design Questions for Max

Site and orientation. Is there a real parcel? The plan assumes the mountain view is to the north and a gentle slope. A view to the west or south would mean rotating the courtyard. A steeper lot could become the gentle split (living pavilion 2 to 3 steps down).

Size. Trimmed from 5,952 to 5,272 SF (smaller kids' rooms and Jack-and-Jill, a 36 × 28 courtyard, tighter dining and living, and an open-air south walkway). Further options if needed: drop the two kids' entry vestibules into the rooms, or fold the tatami room into the west engawa. Any of these gets toward 5,000 to 5,400 SF.

Guest strategy. Kids' Room 2 is the guest room and uses the Guest / Pool Bath across the engawa. Do you want a separate guest suite instead (for example, the tatami room with its own bath), or a casita by the pool?

Fire. The plan uses a slim linear gas fire in the living room (no stone fireplace) and a wood-burning sunken fire pit outside. Is that the right balance? Is a wood stove or sauna stove allowed in your wildfire zone?

Climate and snow. Deep, low eaves and a butterfly valley need snow-load engineering and heated valley gutters. Confirm the snow region, and whether you prefer a single low shed roof over the butterfly.

Budget and level of finish. How far to push the details: hinoki, Calacatta, pocketing steel-framed glass, rammed earth? Each has a lower-cost stand-in.

Water and wastewater. Is there municipal water at the road, or is the well the backup? A perc test will size the drain field and confirm whether a conventional septic tank or an aerobic treatment unit is needed.