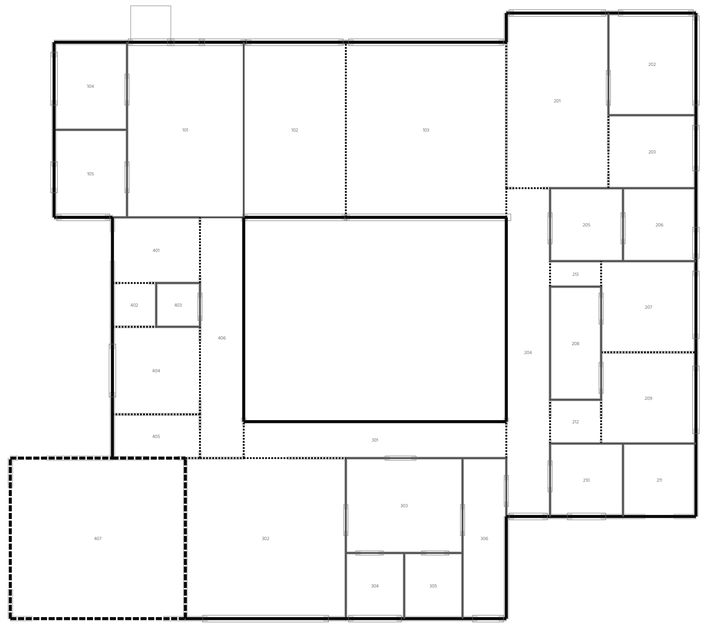


## 1 WALL FRAMING PLAN

SCALE: 3/32" = 1'-0"

### WALL TYPES

| TYPE | DESCRIPTION | BUILD-UP | LENGTH |
|---|---|---|---|
| W1 | AAC Block Exterior Wall | 200 mm AAC block, RC lintels + stiffeners, render + lime plaster or charred-timber rainscreen | 438 ft |
| W2 | AAC Block Wet Wall | 100 mm AAC block, cement render, waterproof membrane in wet zones | 370 ft |
| W3 | Light-Gauge Steel Stud Partition | 92 mm LGS studs @ 400 mm o.c., 12 mm gypsum each side, acoustic insulation | 179 ft |
| W4 | Double-Stud Isolation Wall (STC 60+) | 2 x 92 mm LGS on separate tracks, 25 mm gap, 2 x 16 mm gypsum + mineral wool each side | 92 ft |

### WALL LEGEND

- W1 AAC exterior wall 200 mm
- W2 AAC wet-room wall 100 mm
- W3 LGS stud partition
- W4 Double-stud isolation (Studio)
- L1 RC lintel over opening




## 2 ROOF FRAMING PLAN

SCALE: 3/32" = 1'-0"

### ROOF FRAMING SCHEDULE

| MARK | MEMBER | SECTION / SPEC | QTY |
|---|---|---|---|
| R1 | Steel rafter | H-150 x 75 x 5 x 7, SS400, @ 1.2 m, cantilevers to eaves | 84 |
| P1 | C-purlin | C-100 x 50 x 20 x 2.3, @ 1.1 m max | 60 |
| SK | Skylight trimmer | RHS 100 x 50 x 3.2 frame | 4 |
| -- | Roof deck | Standing seam 0.5 mm AZ150 + 75 mm PIR + underlay | 6 |
| -- | Connections | Rafter to RB1 via cast-in plate 200 x 200 x 12 + 4-M16 anchors | - |
| -- | Corrosion | Hot-dip galvanized or 2-coat epoxy (humid mountain climate) | - |
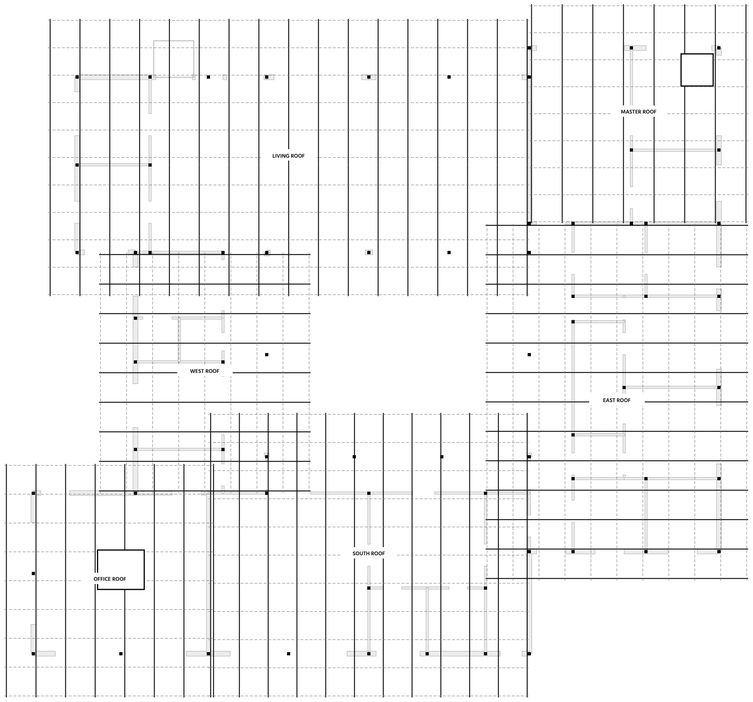
### ROOF FRAMING LEGEND

- Steel rafter R1
- C-purlin P1
- Column below (bearing)

# WEBERMAN RESIDENCE

Mountain courtyard house, Thailand
Owner: Max Weberman

ISSUE

**Design Development**

**NOT FOR CONSTRUCTION**

DATE
11 Oct 2026

SCALE
3/32" = 1'-0"

MODEL
bim.json (from plan.json)

UNITS
Feet + inches (mm for members)

REVISION
DD-01

FRAMING NOTES

Interior LGS: 0.75 mm BMT studs, deflection head track at slab/beam.

AAC: thin-bed mortar; RC stiffener columns 100 x wall width at max 3 m and at openings > 2 m.

Studio double-stud walls on separate tracks + resilient ceiling (STC 60+).

SHEET TITLE

**Wall Framing + Roof Framing Plans**

SHEET

**S-102**