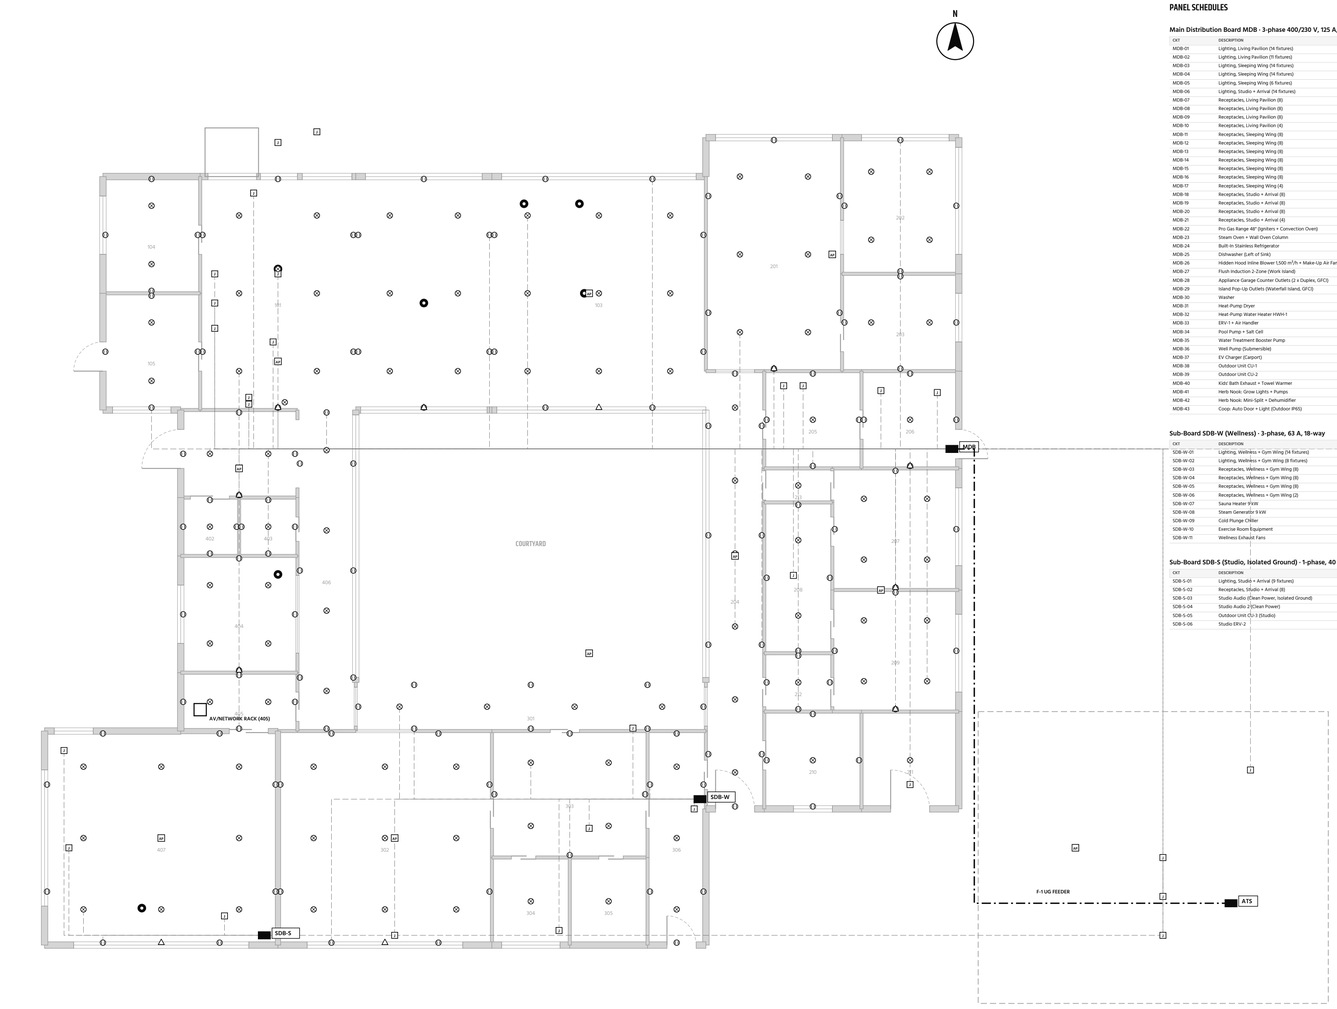


ELECTRICAL LEGEND

- Duplex receptacle 16 A (RCBO in wet areas)
- LED downlight 2700 K dimmable
- Decorative pendant / lantern
- Dedicated circuit / equipment connection
- Data outlet 2 x Cat6A
- Wi-Fi access point (PoE)
- Distribution board
- Circuit home run (conduit in ceiling)
- Underground feeder

PANEL SCHEDULES

Main Distribution Board MDB · 3-phase 400/230 V, 125 A, 36-way, RCBO protected

CKT	DESCRIPTION	LOAD	BREAKER
MDB-01	Lighting, Living Pavilion (14 fixtures)	140 W	10 A RCBO
MDB-02	Lighting, Living Pavilion (11 fixtures)	110 W	10 A RCBO
MDB-03	Lighting, Sleeping Wing (14 fixtures)	140 W	10 A RCBO
MDB-04	Lighting, Sleeping Wing (14 fixtures)	140 W	10 A RCBO
MDB-05	Lighting, Sleeping Wing (6 fixtures)	60 W	10 A RCBO
MDB-06	Lighting, Studio + Arrival (14 fixtures)	140 W	10 A RCBO
MDB-07	Receptacles, Living Pavilion (B)	1,800 VA	16 A RCBO
MDB-08	Receptacles, Living Pavilion (B)	1,800 VA	16 A RCBO
MDB-09	Receptacles, Living Pavilion (B)	1,800 VA	16 A RCBO
MDB-10	Receptacles, Living Pavilion (K)	1,800 VA	16 A RCBO
MDB-11	Receptacles, Sleeping Wing (B)	1,800 VA	16 A RCBO
MDB-12	Receptacles, Sleeping Wing (B)	1,800 VA	16 A RCBO
MDB-13	Receptacles, Sleeping Wing (B)	1,800 VA	16 A RCBO
MDB-14	Receptacles, Sleeping Wing (B)	1,800 VA	16 A RCBO
MDB-15	Receptacles, Sleeping Wing (B)	1,800 VA	16 A RCBO
MDB-16	Receptacles, Sleeping Wing (B)	1,800 VA	16 A RCBO
MDB-17	Receptacles, Sleeping Wing (K)	1,800 VA	16 A RCBO
MDB-18	Receptacles, Studio + Arrival (B)	1,800 VA	16 A RCBO
MDB-19	Receptacles, Studio + Arrival (B)	1,800 VA	16 A RCBO
MDB-20	Receptacles, Studio + Arrival (B)	1,800 VA	16 A RCBO
MDB-21	Receptacles, Studio + Arrival (K)	1,800 VA	16 A RCBO
MDB-22	Pro Gas Range 48" (Ignites + Convection Oven)	18 kW	16 A
MDB-23	Steam Oven + Wall Oven Column	6.5 kW	32 A 2P
MDB-24	Built-In Stainless Refrigerator	0.6 kW	16 A
MDB-25	Dishwasher (Left of Sink)	1.8 kW	16 A
MDB-26	Hidden Hood Inline Blower 1,500 m³/h + Make-Up Air Fan	0.8 kW	16 A
MDB-27	Flush Induction 2-Zone (Work Island)	3.7 kW	20 A
MDB-28	Appliance Garage Counter Outlets (2 x Duplex, GFCI)	1.8 kW	16 A RCBO
MDB-29	Island Pop-Up Outlets (Waterfall Island, GFCI)	1.8 kW	16 A RCBO
MDB-30	Washer	2.2 kW	16 A
MDB-31	Heat-Pump Dryer	1.2 kW	16 A
MDB-32	Heat-Pump Water Heater HWH-1	1.5 kW	16 A
MDB-33	ERV-1 + Air Handler	0.4 kW	10 A
MDB-34	Pool Pump + Salt Cell	1.5 kW	16 A
MDB-35	Water Treatment Booster Pump	1.1 kW	16 A
MDB-36	Well Pump (Submersible)	1.5 kW	16 A
MDB-37	EV Charger (Carport)	7.4 kW	32 A 2P
MDB-38	Outdoor Unit CU-1	9.0 kW	3P 25 A
MDB-39	Outdoor Unit CU-2	12.0 kW	3P 25 A
MDB-40	Kids' Bath Exhaust + Towel Warmer	0.2 kW	10 A
MDB-41	Herb Nook: Grow Lights + Pumps	1.2 kW	16 A RCBO
MDB-42	Herb Nook: Mini-Split + Dehumidifier	1.2 kW	16 A
MDB-43	Coop: Auto Door + Light (Outdoor IP65)	0.1 kW	10 A RCBO

Sub-Board SDB-W (Wellness) · 3-phase, 63 A, 18-way

CKT	DESCRIPTION	LOAD	BREAKER
SDB-W-01	Lighting, Wellness + Gym Wing (14 fixtures)	140 W	10 A RCBO
SDB-W-02	Lighting, Wellness + Gym Wing (8 fixtures)	80 W	10 A RCBO
SDB-W-03	Receptacles, Wellness + Gym Wing (B)	1,800 VA	16 A RCBO
SDB-W-04	Receptacles, Wellness + Gym Wing (B)	1,800 VA	16 A RCBO
SDB-W-05	Receptacles, Wellness + Gym Wing (B)	1,800 VA	16 A RCBO
SDB-W-06	Receptacles, Wellness + Gym Wing (2)	1,800 VA	16 A RCBO
SDB-W-07	Sauna Heater 9 kW	9.0 kW	3P 16 A
SDB-W-08	Steam Generator 9 kW	9.0 kW	3P 16 A
SDB-W-09	Cold Plunge Chiller	1.2 kW	16 A
SDB-W-10	Exercise Room Equipment	2.0 kW	16 A
SDB-W-11	Wellness Exhaust Fans	0.3 kW	10 A

Sub-Board SDB-S (Studio, Isolated Ground) · 1-phase, 40 A, 12-way

CKT	DESCRIPTION	LOAD	BREAKER
SDB-S-01	Lighting, Studio + Arrival (9 fixtures)	90 W	10 A RCBO
SDB-S-02	Receptacles, Studio + Arrival (B)	1,800 VA	16 A RCBO
SDB-S-03	Studio Audio (Clean Power, Isolated Ground)	2.0 kW	16 A IG
SDB-S-04	Studio Audio 2 (Clean Power)	2.0 kW	16 A IG
SDB-S-05	Outdoor Unit CU-3 (Studio)	4.5 kW	25 A
SDB-S-06	Studio ERV-2	0.2 kW	10 A

1 **POWER + LIGHTING PLAN**

SCALE: 1/8" = 1'-0"

WEBERMAN RESIDENCE

Mountain courtyard house, Thailand
Owner: Max Weberman

ISSUE

Design Development

NOT FOR CONSTRUCTION

DATE
11 Oct 2026

SCALE
1/8" = 1'-0"

MODEL
bim.json (from plan.json)

UNITS
Feet + inches (mm for members)

REVISION
DD-01

ELECTRICAL NOTES

PEA 3-phase 400/230 V service; TN-C-S earthing per EIT standard, < 5 ohm.

RCBO (30 mA) on all receptacle, wet-area and outdoor circuits.

Light switch style is an open item (Round 2); switching and dimming zones to be shown at CD.

Wire sizes per EIT 2001-56 at CD; load calc pending equipment selection.

KITCHEN (ROUND 1)

Pro gas range 16 A (igniters); flush induction 20 A; steam + wall oven 32 A 2P; built-in stainless fridge 16 A; hood blower + MUA 16 A.

GFCI counter outlets at the appliance garage and island pop-ups; linear suspended LED on DALI. Detail on A-401.

SHEET TITLE
Power + Lighting Plan

SHEET
E-101