WEBERMAN RESIDENCE

Design Development Concept Construction Set

Mountain courtyard house, Thailand · Owner: Max Weberman · Issue DD-01, 11 Oct 2026

DESIGN DEVELOPMENT, NOT FOR CONSTRUCTION

SHEET INDEX

SHEET	TITLE	SCALE
G-001	Cover Sheet + Sheet Index	As Noted
G-002	Sustainability Summary	NTS
G-003	Construction Standards (Thai vs Western)	NTS
A-101	Floor Plan (Dimensioned)	1/8" = 1'-0"
A-102	Roof Plan	1/8" = 1'-0"
A-201	Exterior Elevations	1/8" = 1'-0"
A-301	Building Sections	3/16" = 1'-0"
A-401	Kitchen Plan + Elevations	1/4" = 1'-0"
S-101	Foundation + Structural Plan	1/8" = 1'-0"
S-102	Wall Framing + Roof Framing Plans	3/32" = 1'-0"
E-101	Power + Lighting Plan	1/8" = 1'-0"
P-101	Plumbing + Site Utilities Plan	3/32" = 1'-0"
M-101	HVAC Plan	1/8" = 1'-0"
E-102	Solar PV Plan + Single-Line Diagram	3/32" = 1'-0"
E-103	Controls + Monitoring	NTS
P-102	Rainwater, Irrigation + Kitchen Garden Plan	1/16" = 1'-0"
P-103	Water Source + Treatment	NTS

ONE SHARED MODEL

Every sheet in this set and the interactive 3D model are generated from one data model: plan.json (rooms, walls, openings, roofs, site) extended into bim.json with 1,512 elements in twelve layers (Architecture 82, Structure 369, Framing 142, Roof 153, Electrical 383, Plumbing 160, HVAC 68, Site Utilities 10, Water + Rainwater 29, Solar 48, Controls 46, Landscape + Farm 22). Change the model and both regenerate, so drawings and 3D always match.

PROJECT DATA

Conditioned area	5,272 SF (490 m²), single level
Footprint	94' x 83' around a 36' x 28' courtyard
Structure	RC frame on spread footings, LGS stud walls (fiber-cement + lime plaster), steel roof framing
Roofs	Standing seam: butterfly (Living) + 5 shed roofs, 4-8 ft eaves
Services	PEA 3-phase + solar/battery/generator; well + rainwater; septic + ATU; saltwater pool
Codes (to confirm)	Building Control Act B.E. 2522, Ministerial Regs, EIT electrical standard, DPT 1301/1302/1311

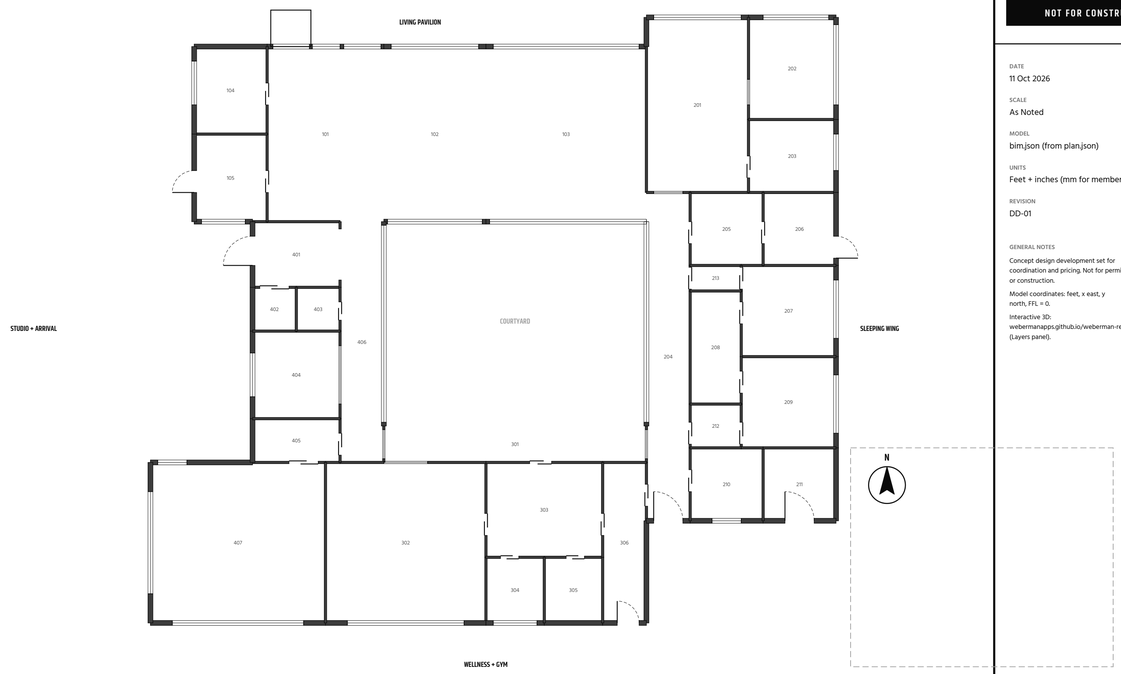

K **KEY PLAN**

SCALE: 3/32" = 1'-0"

ASSUMPTIONS FOR THAI ENGINEER VERIFICATION

1. Allowable soil bearing 10 t/m² and footing depth 1.5 m (no soil test yet). Mountain slope may require piles or stepped footings.
2. RC member sizes (C1 250x250, GB1 200x500, RB1 200x400, S1 125 mm) and rebar are placeholders for a 1-storey frame at about 4.5 m bays.
3. Steel transfer beams TB1 over the 21 ft pocketing glass and frameless corner: assumed W250, deflection limit L/600 for glass.
4. Steel rafters H-150 cantilevering 4-8 ft at eaves; uplift and connection design by engineer (DPT 1311 wind).
5. Electrical: 3-phase 400/230 V PEA service, 125 A main; load calc, cable sizes and RCBO selection to EIT standard at CD.
6. Cooling at about 850 BTU/h per m²; VRF/multi-split outdoor units CU-1/2/3 sized by connected load, not by a heat-load calc.
7. Plumbing pipe sizes by fixture count rule of thumb; septic + ATU and drain field sized for 6 people, perc test required.
8. Rainwater ring, tanks (2 x 19,000 L), well and pool routes are schematic; final routes per survey and civil grading.
9. Saltwater pool: corrosion-resistant fittings, backwash to lined soakaway; bonding/equipotential grid per EIT.

WEBERMAN RESIDENCE

Mountain courtyard house, Thailand
Owner: Max Weberman

ISSUE
Design Development
NOT FOR CONSTRUCTION

DATE
11 Oct 2026

SCALE
As Noted

MODEL
bim.json (from plan.json)

UNITS
Feet + inches (mm for members)

REVISION
DD-01

GENERAL NOTES

Concept design development set for coordination and pricing. Not for permit or construction.

Model coordinates: feet, x east, y north, FFL = 0.

Interactive 3D: webermanapps.github.io/weberman-residence (Layers panel).

SHEET TITLE
Cover Sheet + Sheet Index

SHEET
G-001